





CARNET DE DETAILS


CLOTURE DU RESTAURANT L'ARBRADELIS BARRACHOIS SAINT DENIS




Les plans joints ne sont en aucun cas des plans d'exécution, toutes les côtes et mesures doivent être vérifiées et au besoin modifiées pour la bonne réalisation de ce projet

Plans de principe de la cloture du restaurant Arbradelis au Barachois Saint Denis

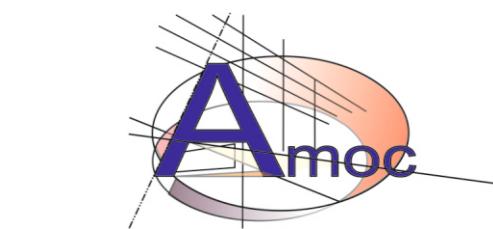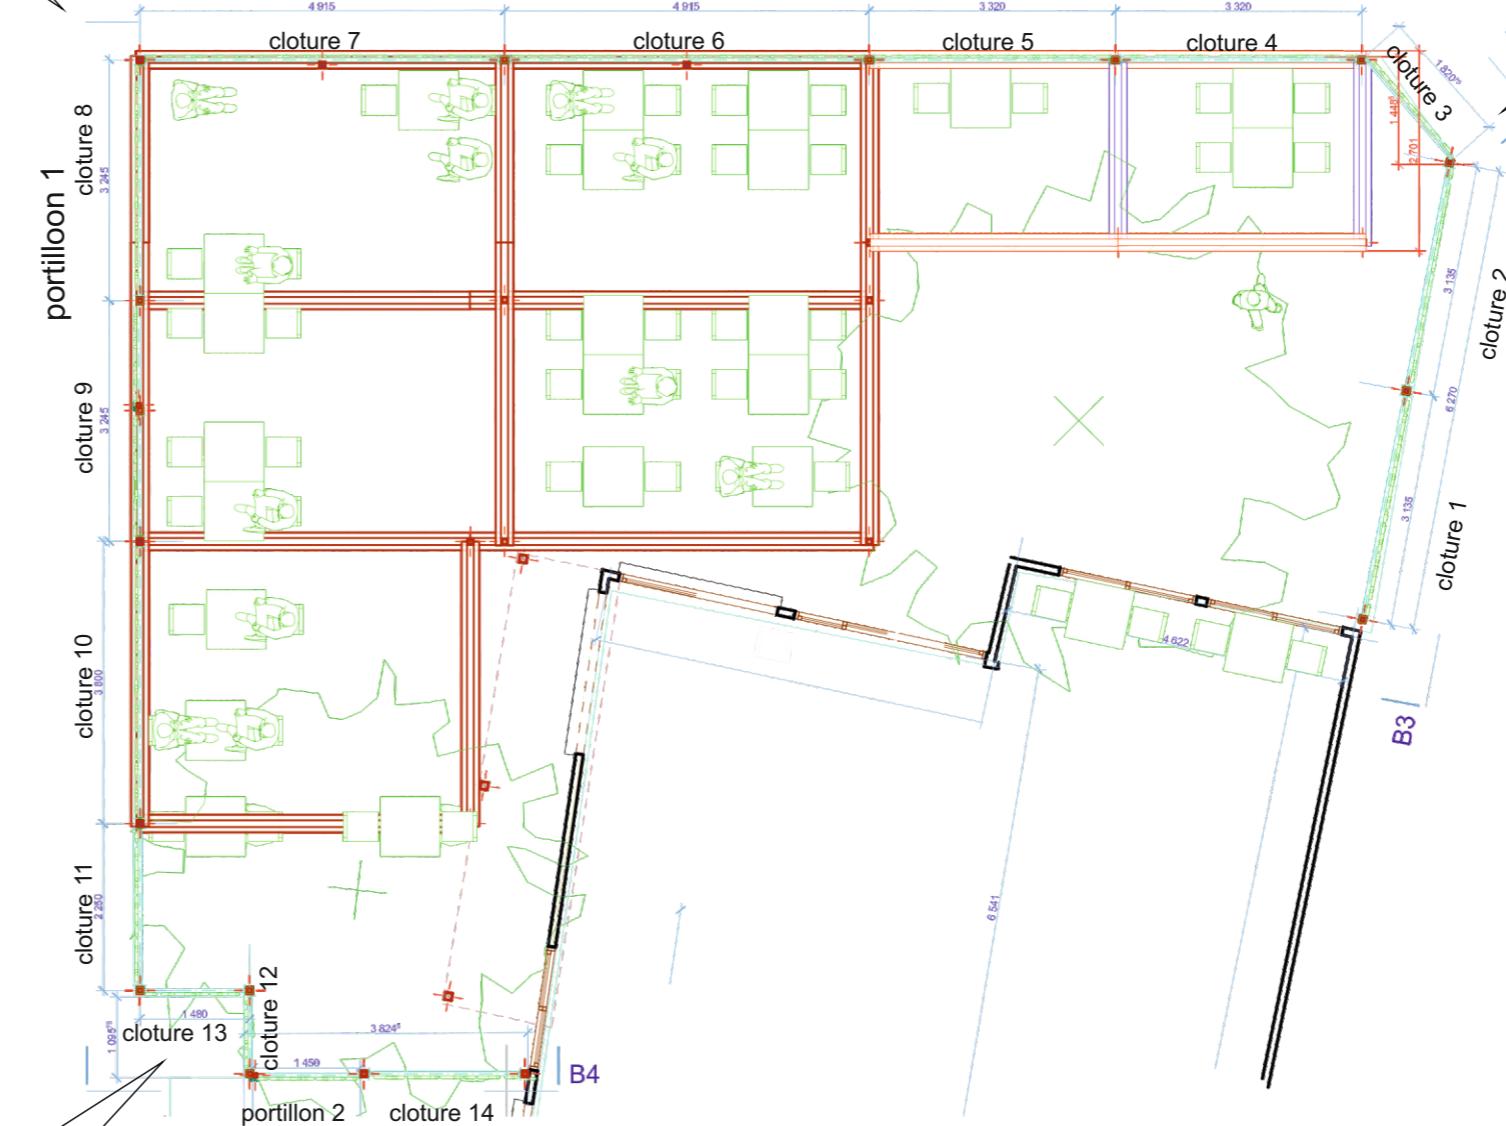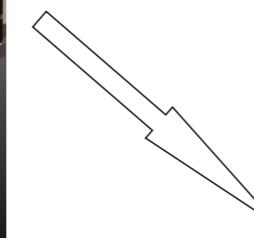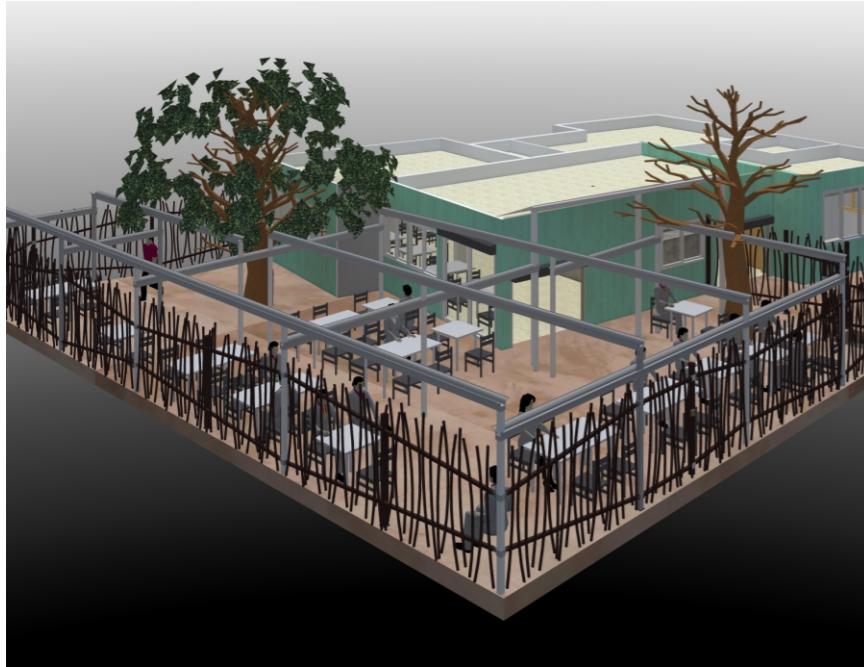






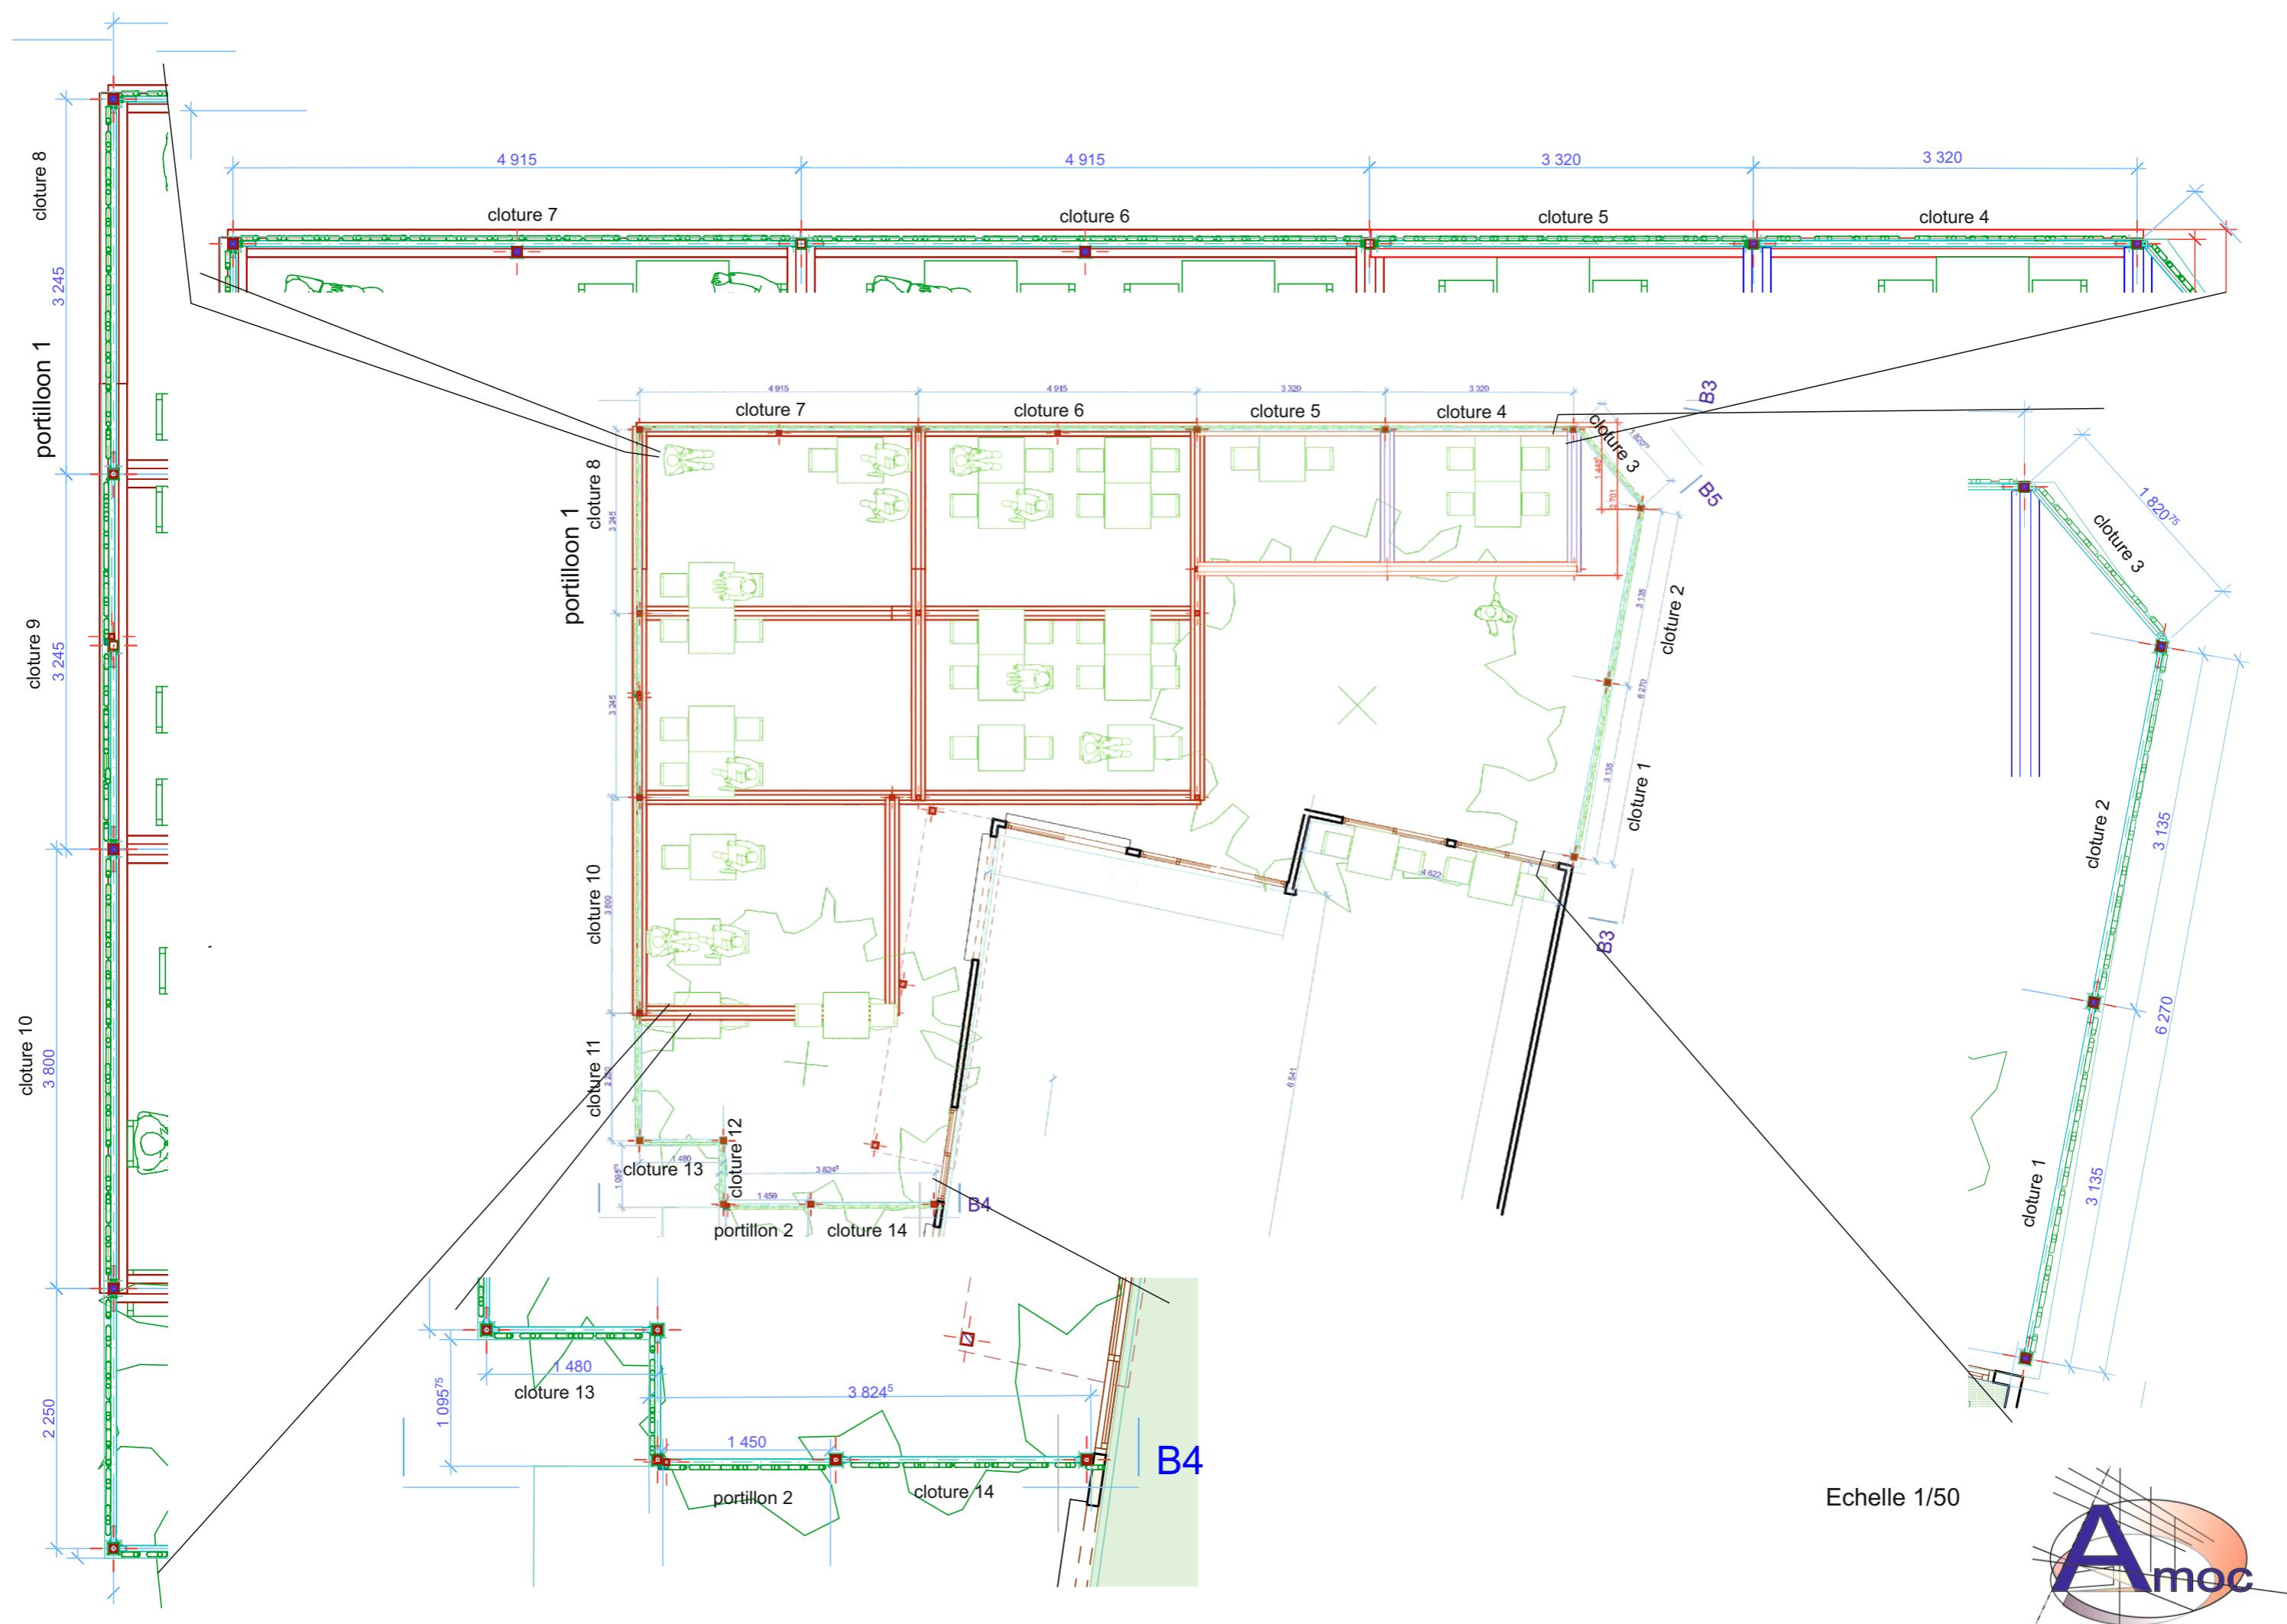




Echelle 1/50

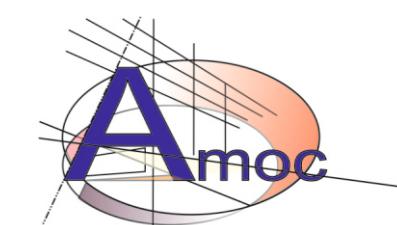


Principe générale

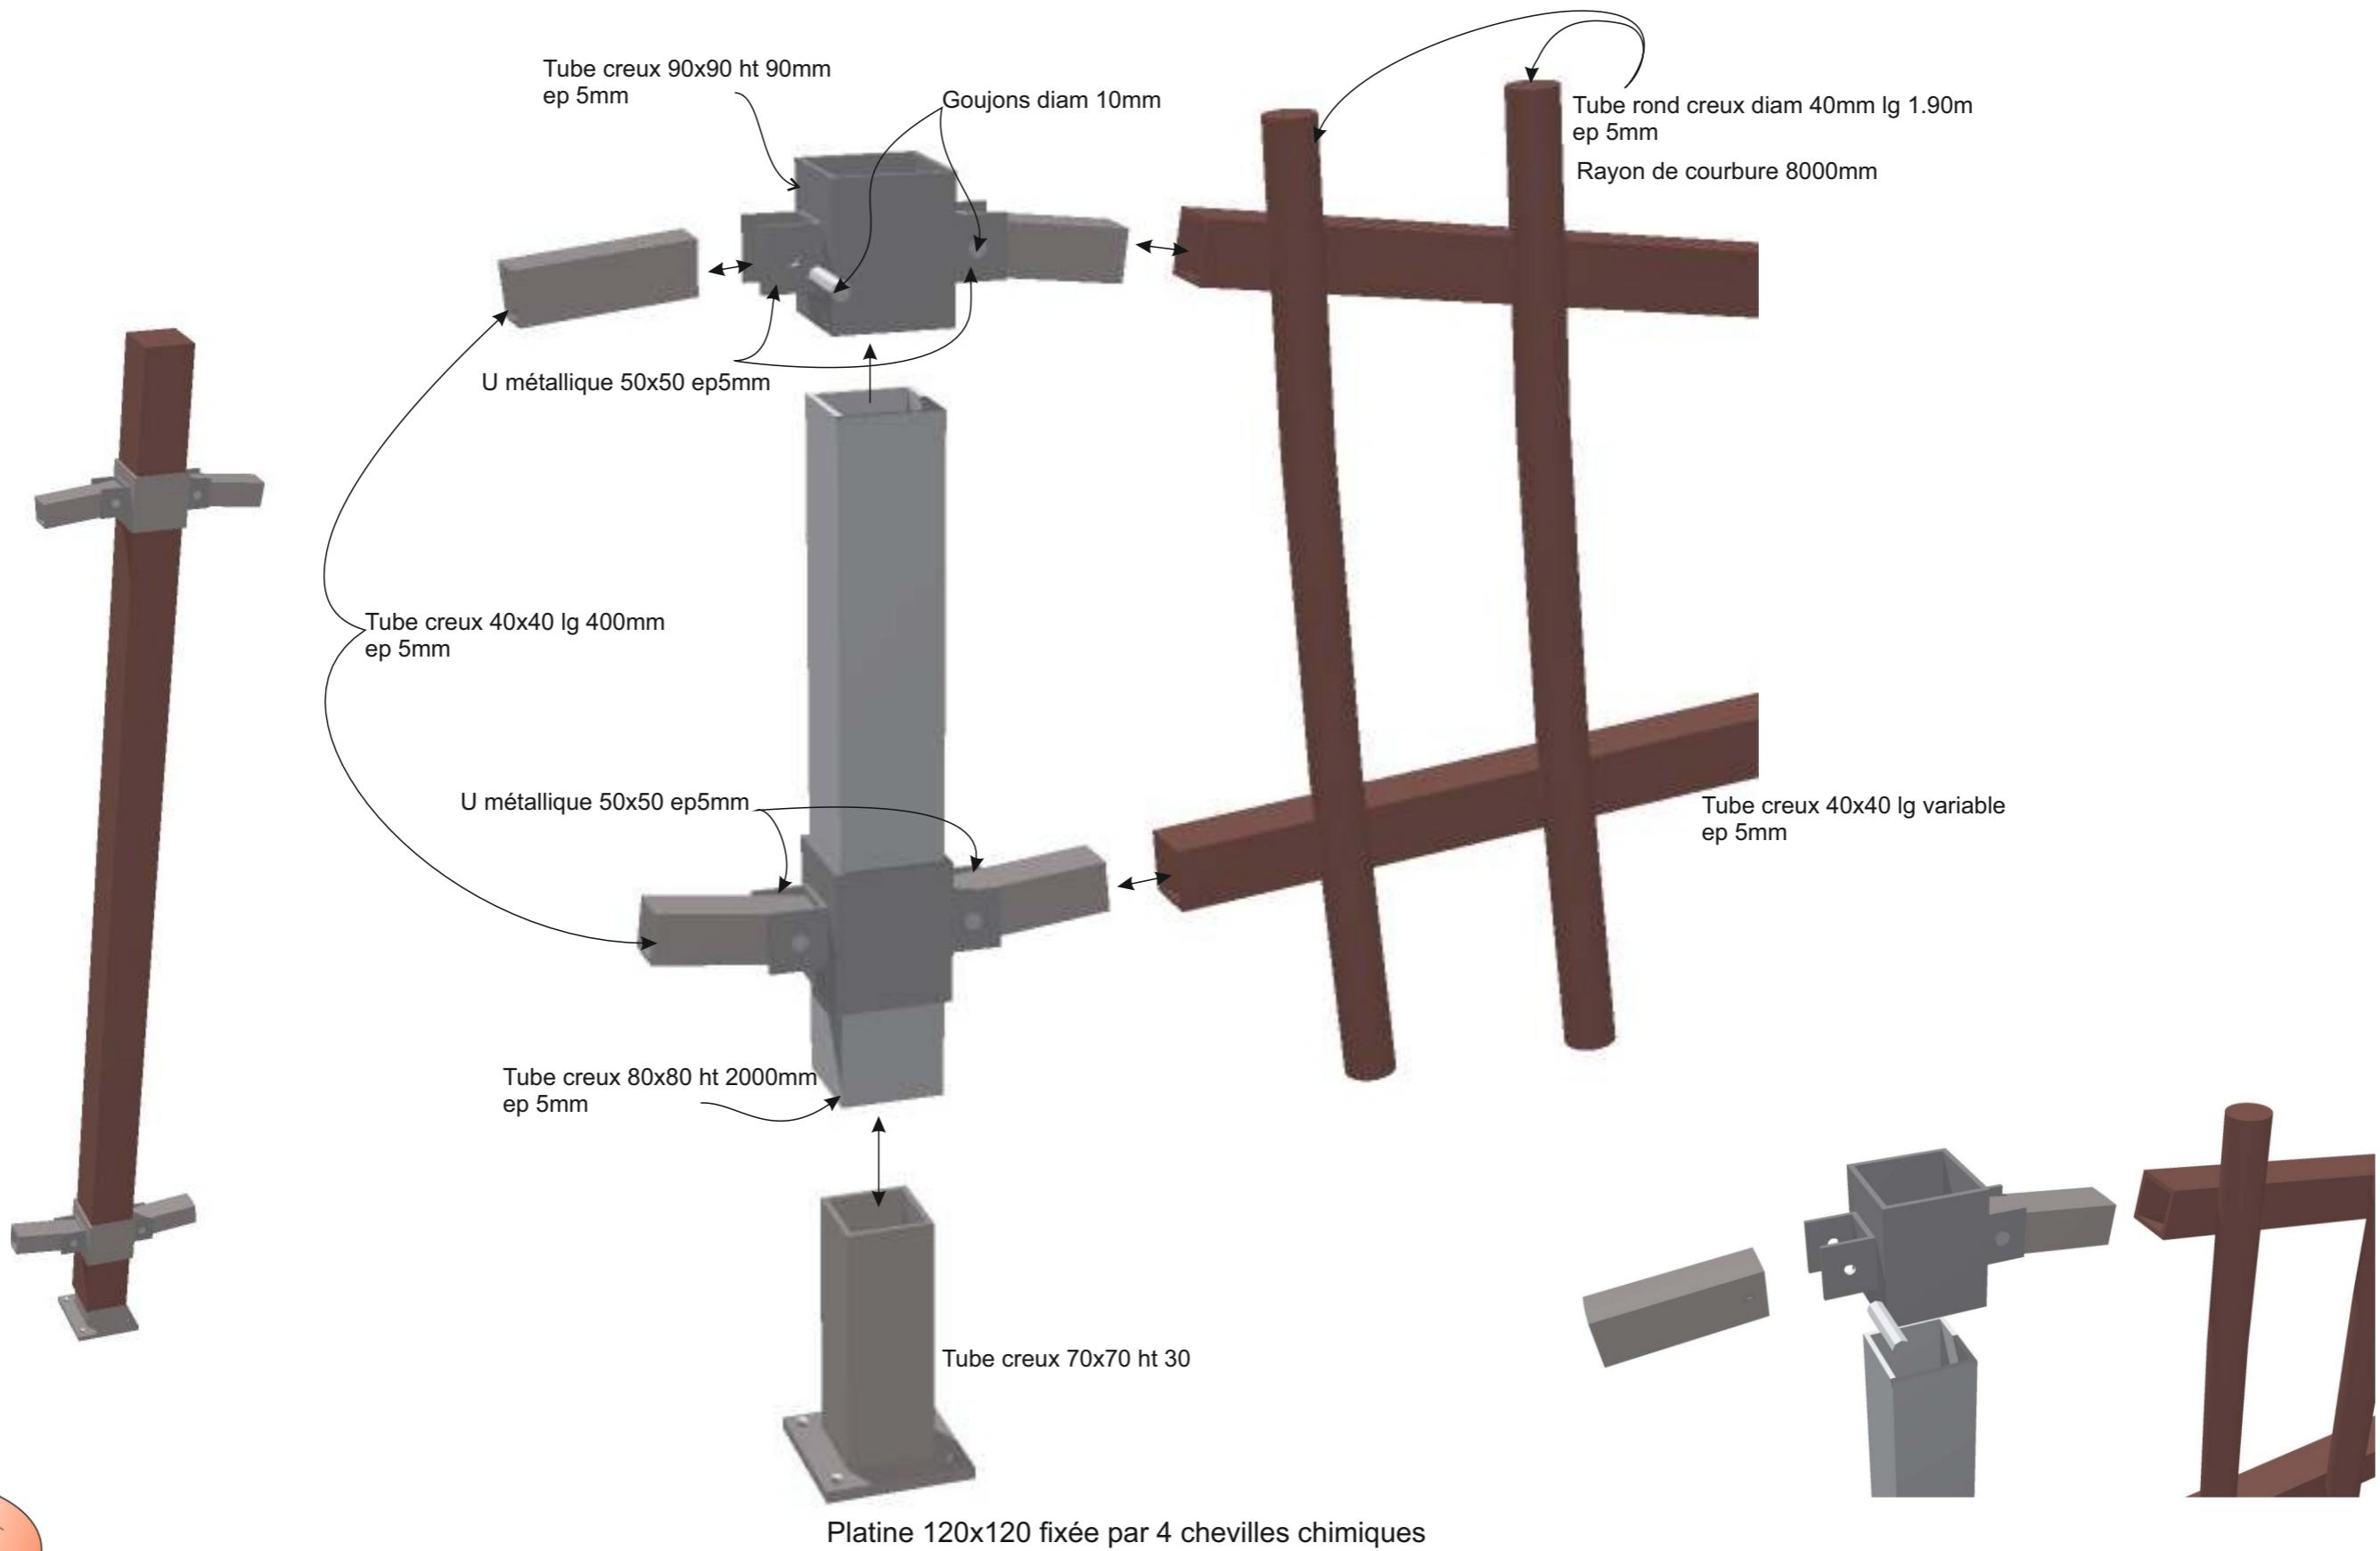

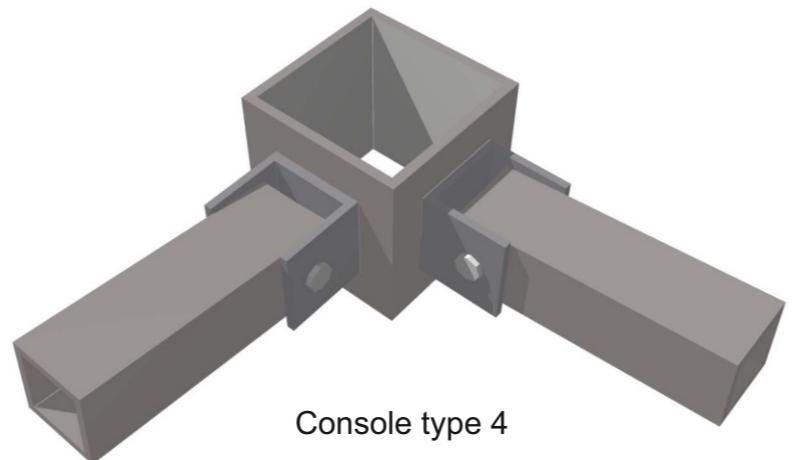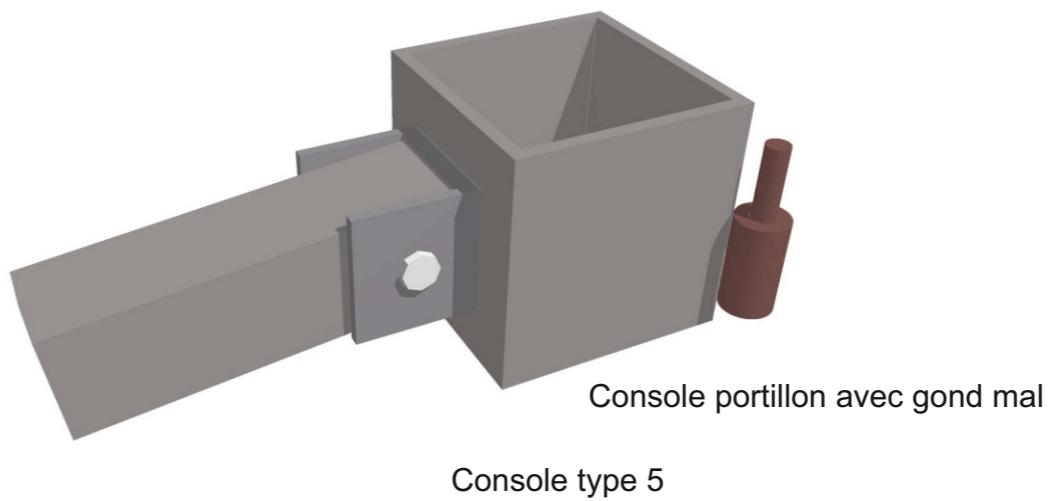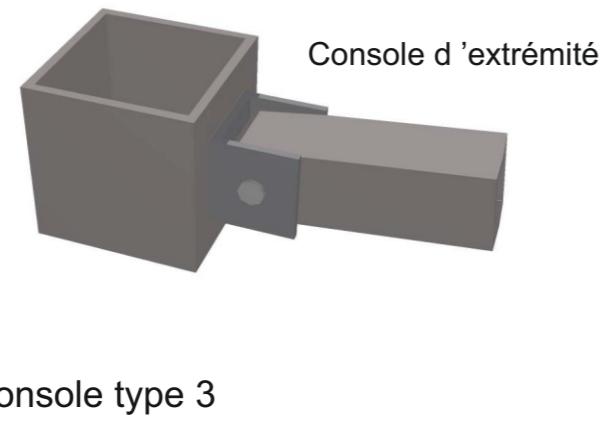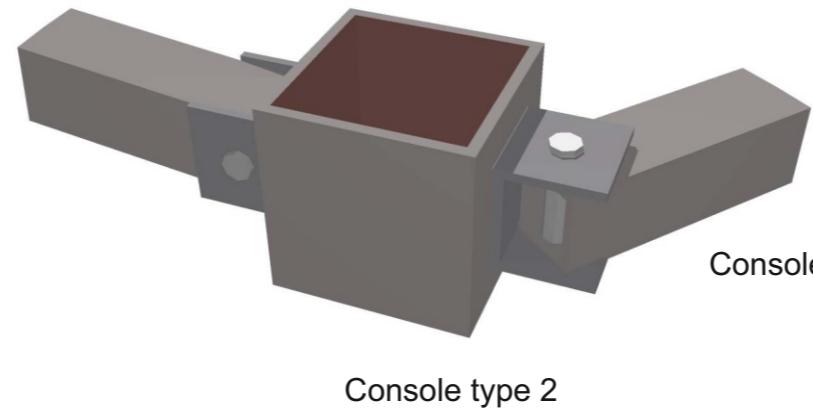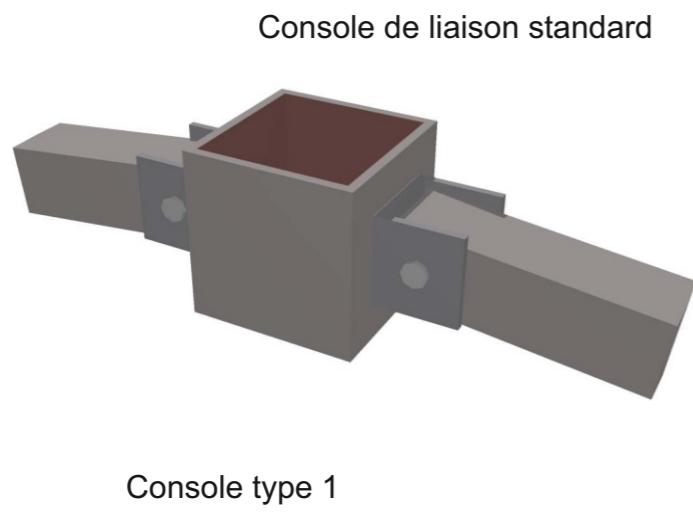

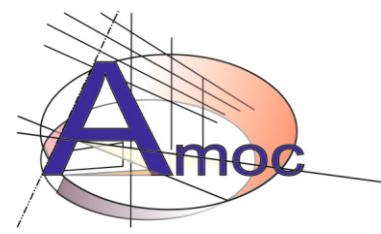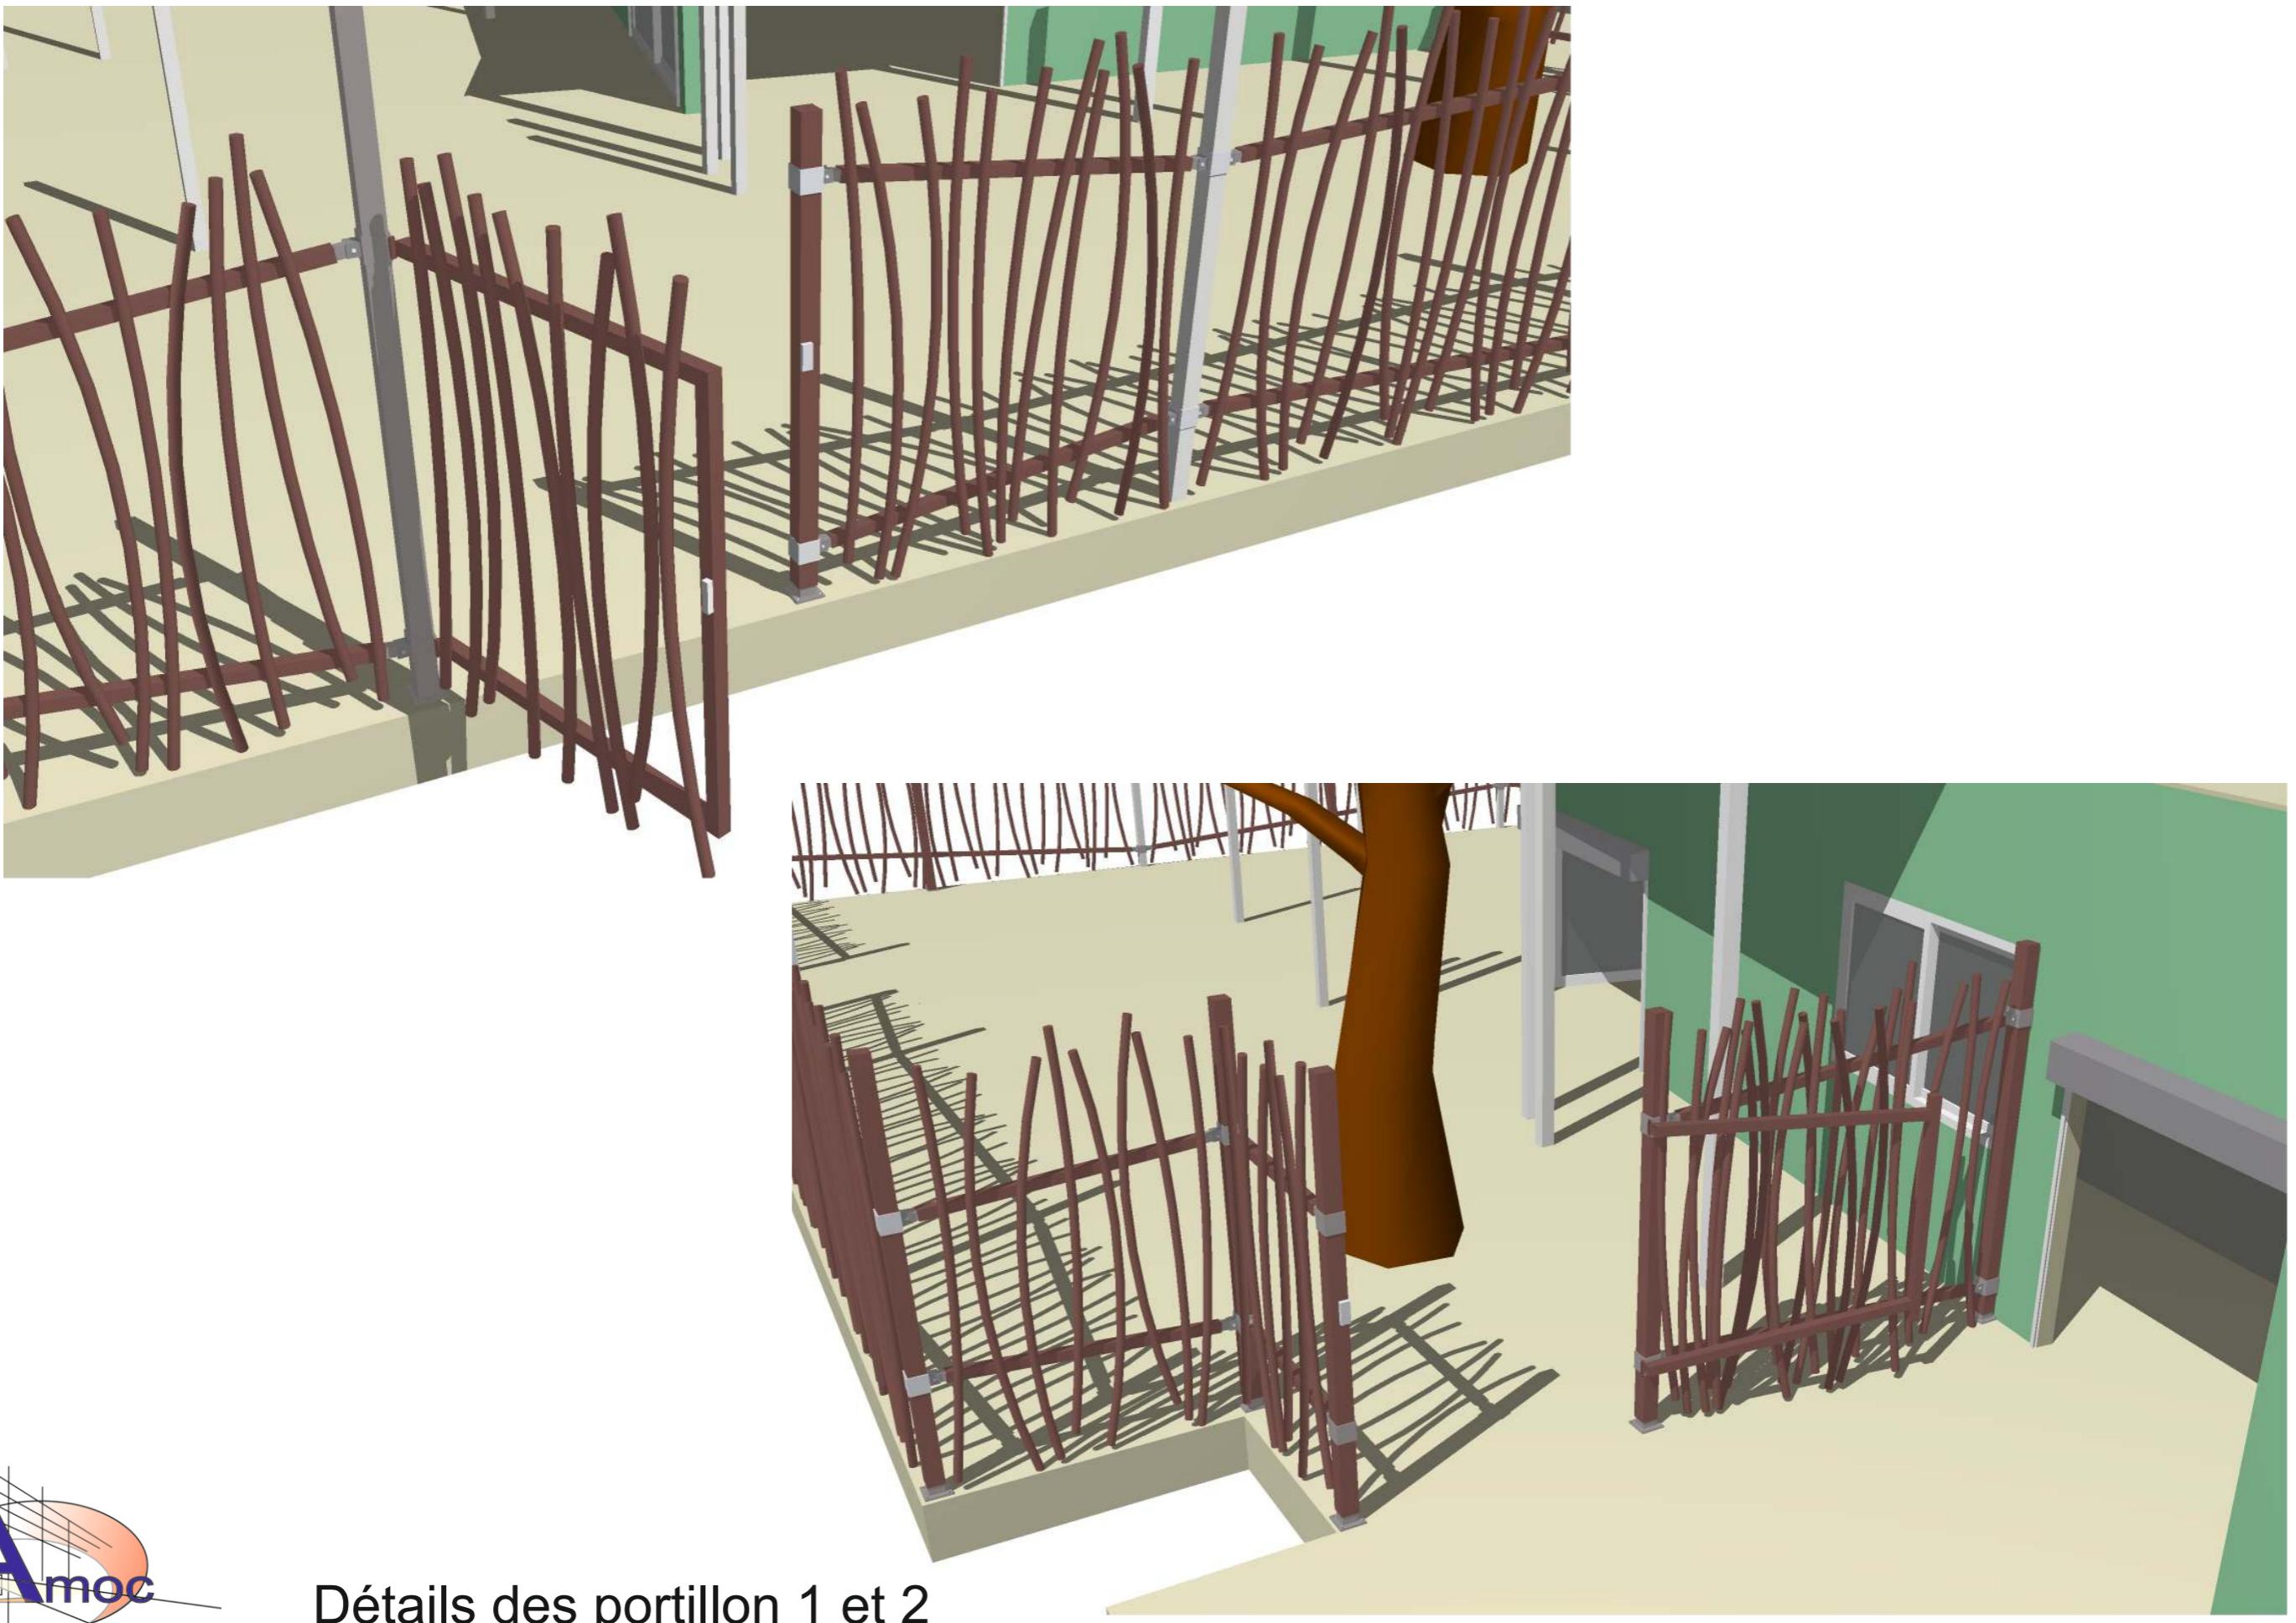

Détails des portillon 1 et 2

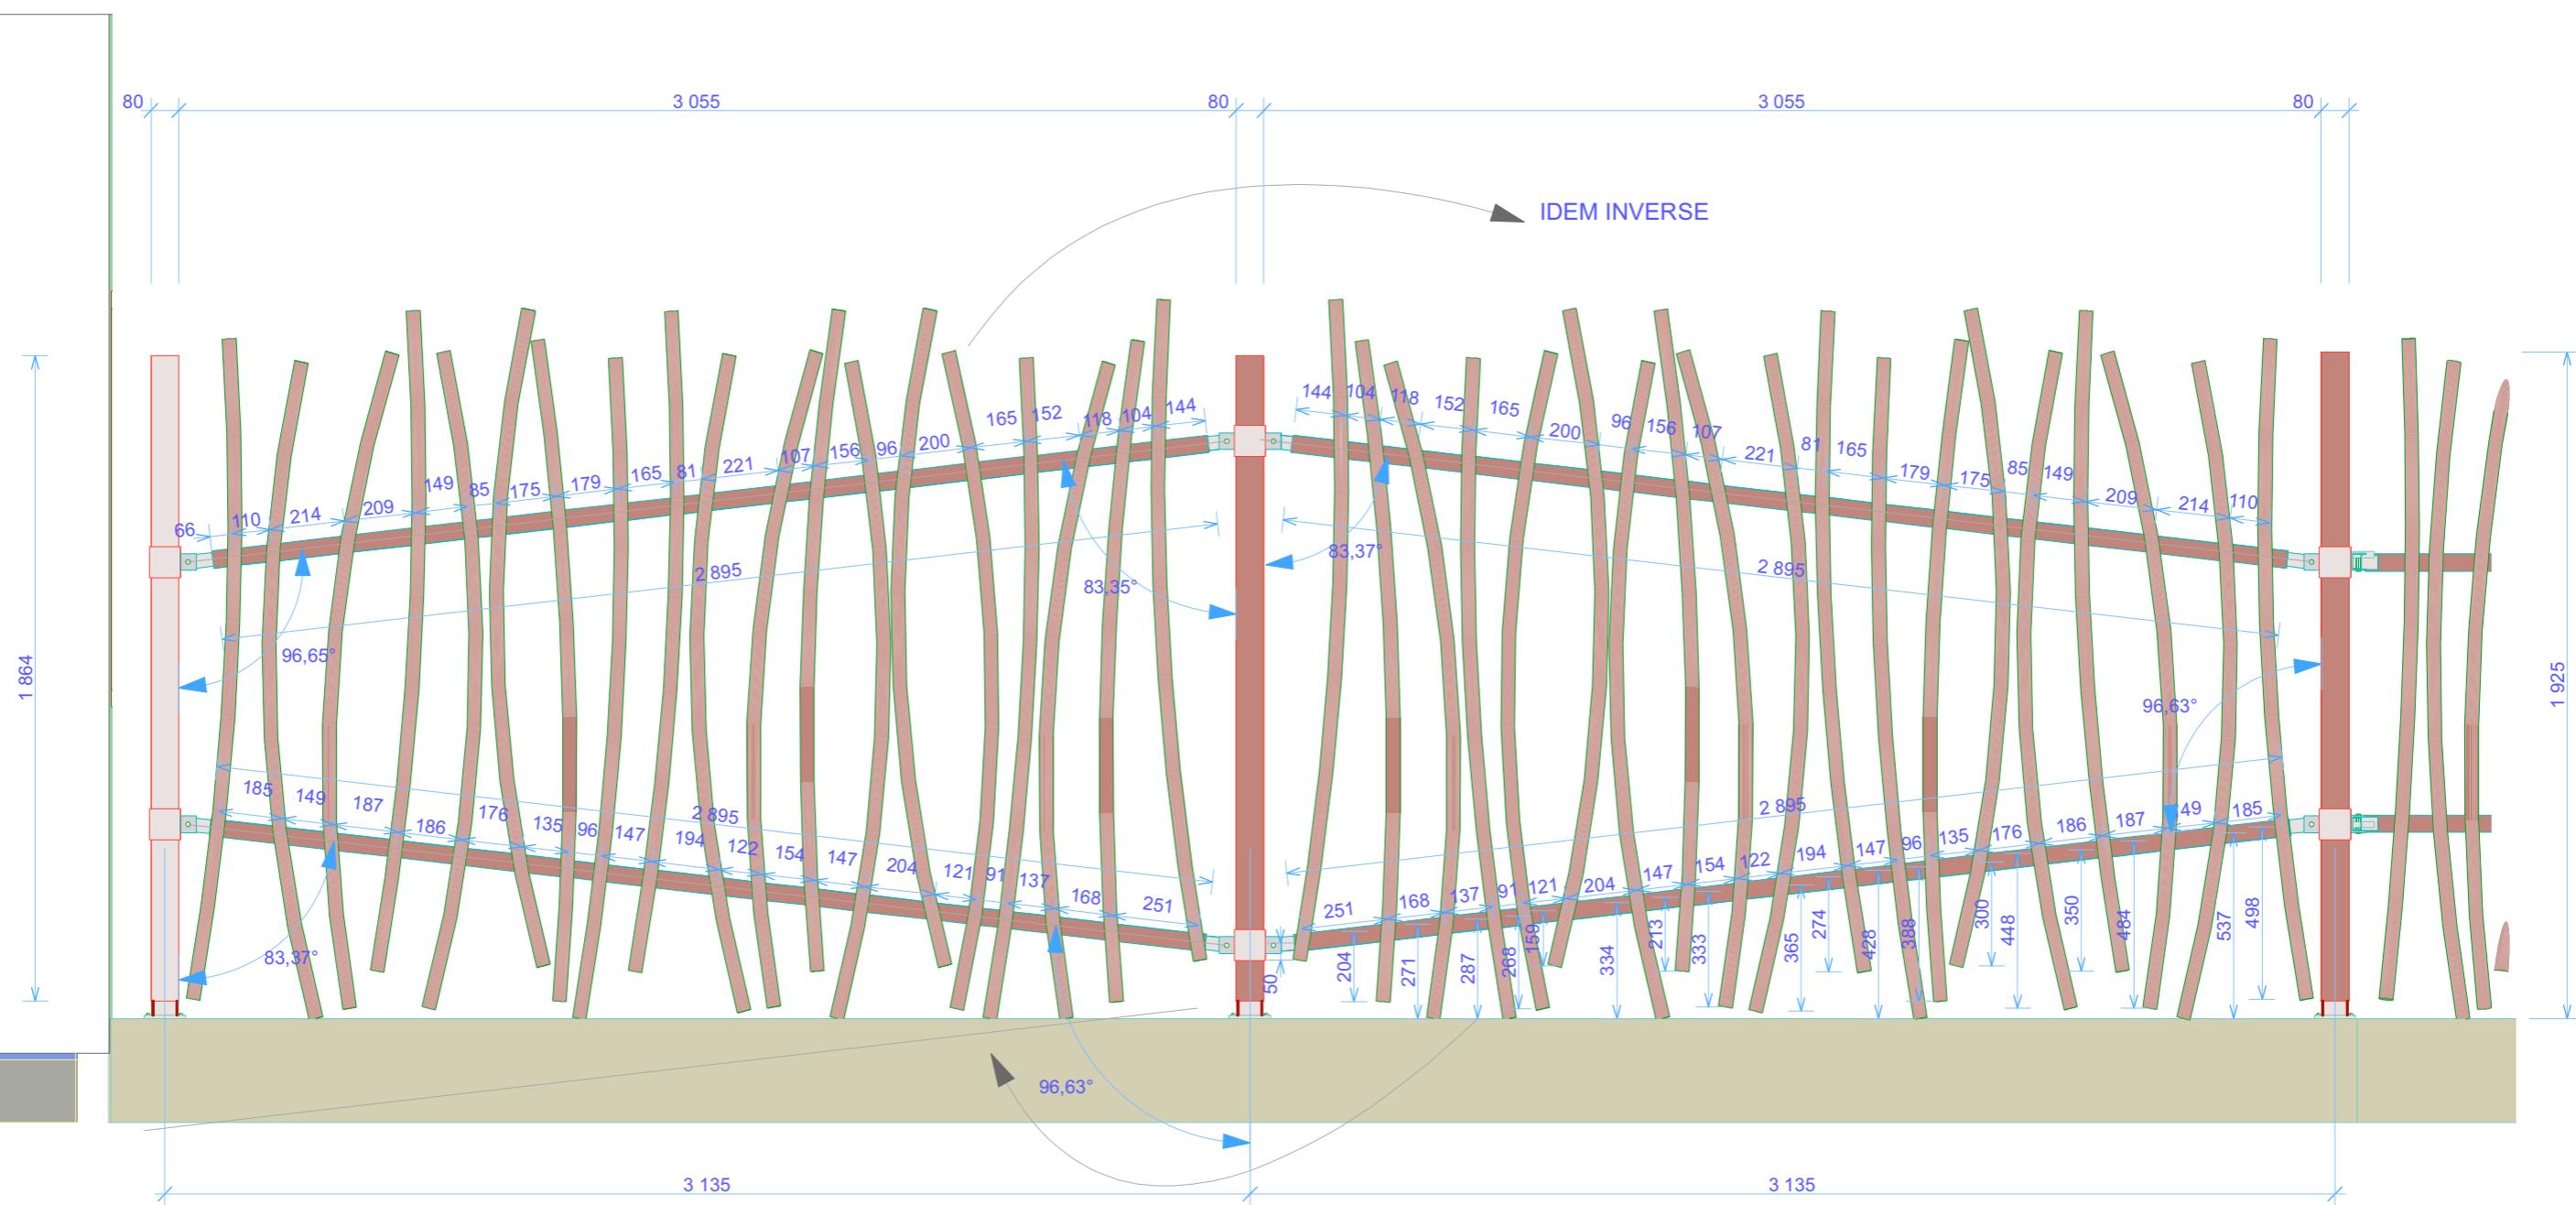

Cloture 1

Cloture 2


Echelle 1/20

- 2 consoles d 'extrémité
 - 2 consoles de liaison
 - 2 poteaux 80x80
 - 3 Pieds de poteau avec platine
 - 2 consoles d 'angle 45° et un poteau prévus dans clôture 3







Détails cloture 3

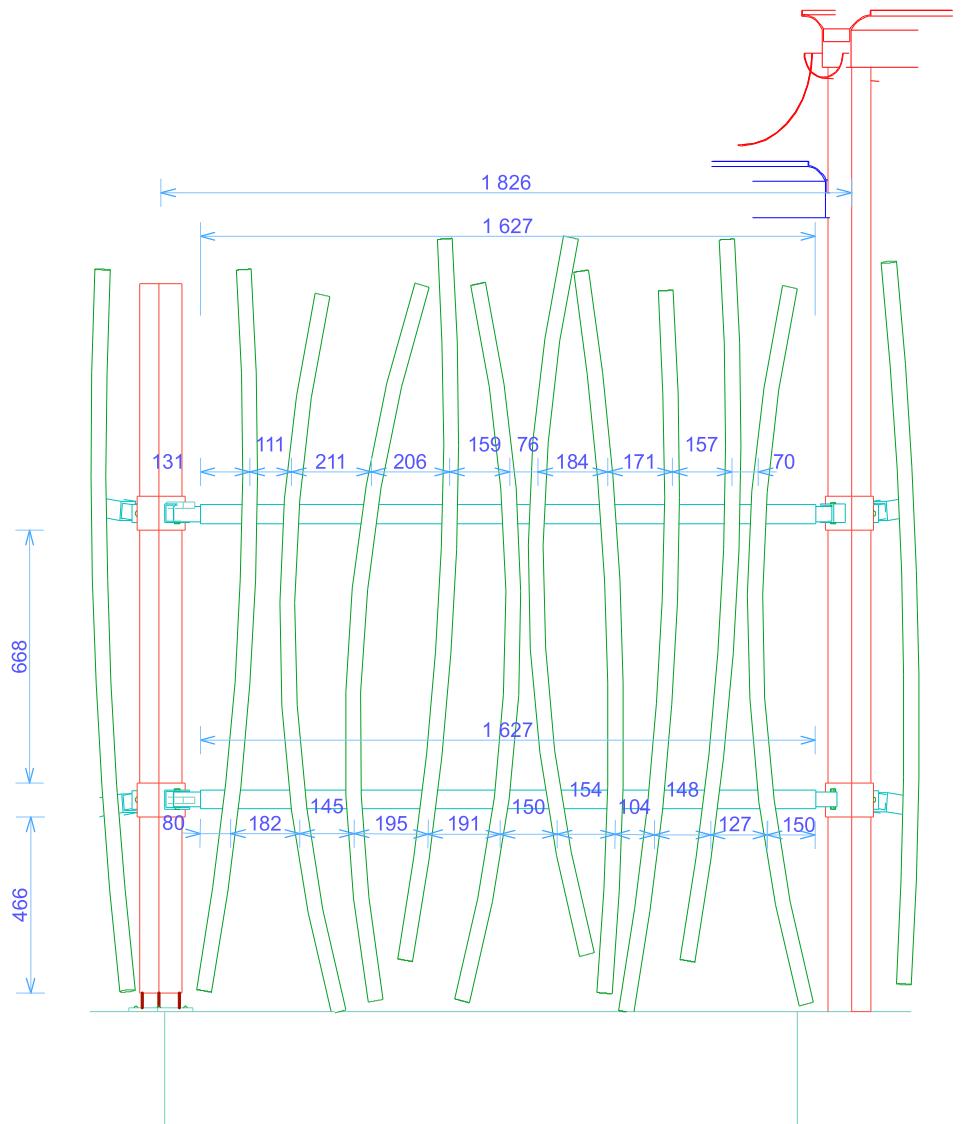

4 consoles d 'angle 45°
1 poteau 80x80
1 pied de poteau sur platine
Le poteau de droite et le pied sont fournis par le storiste

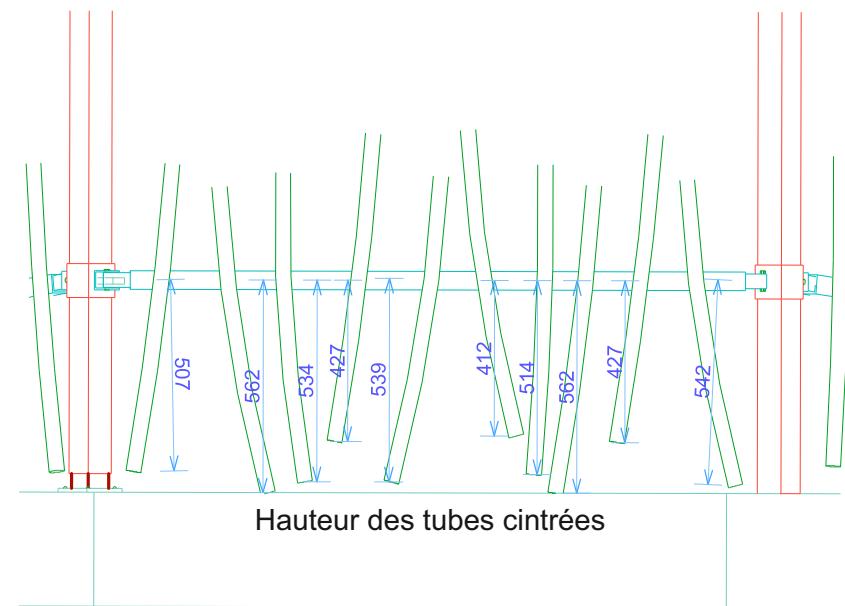

Echelle 1/20

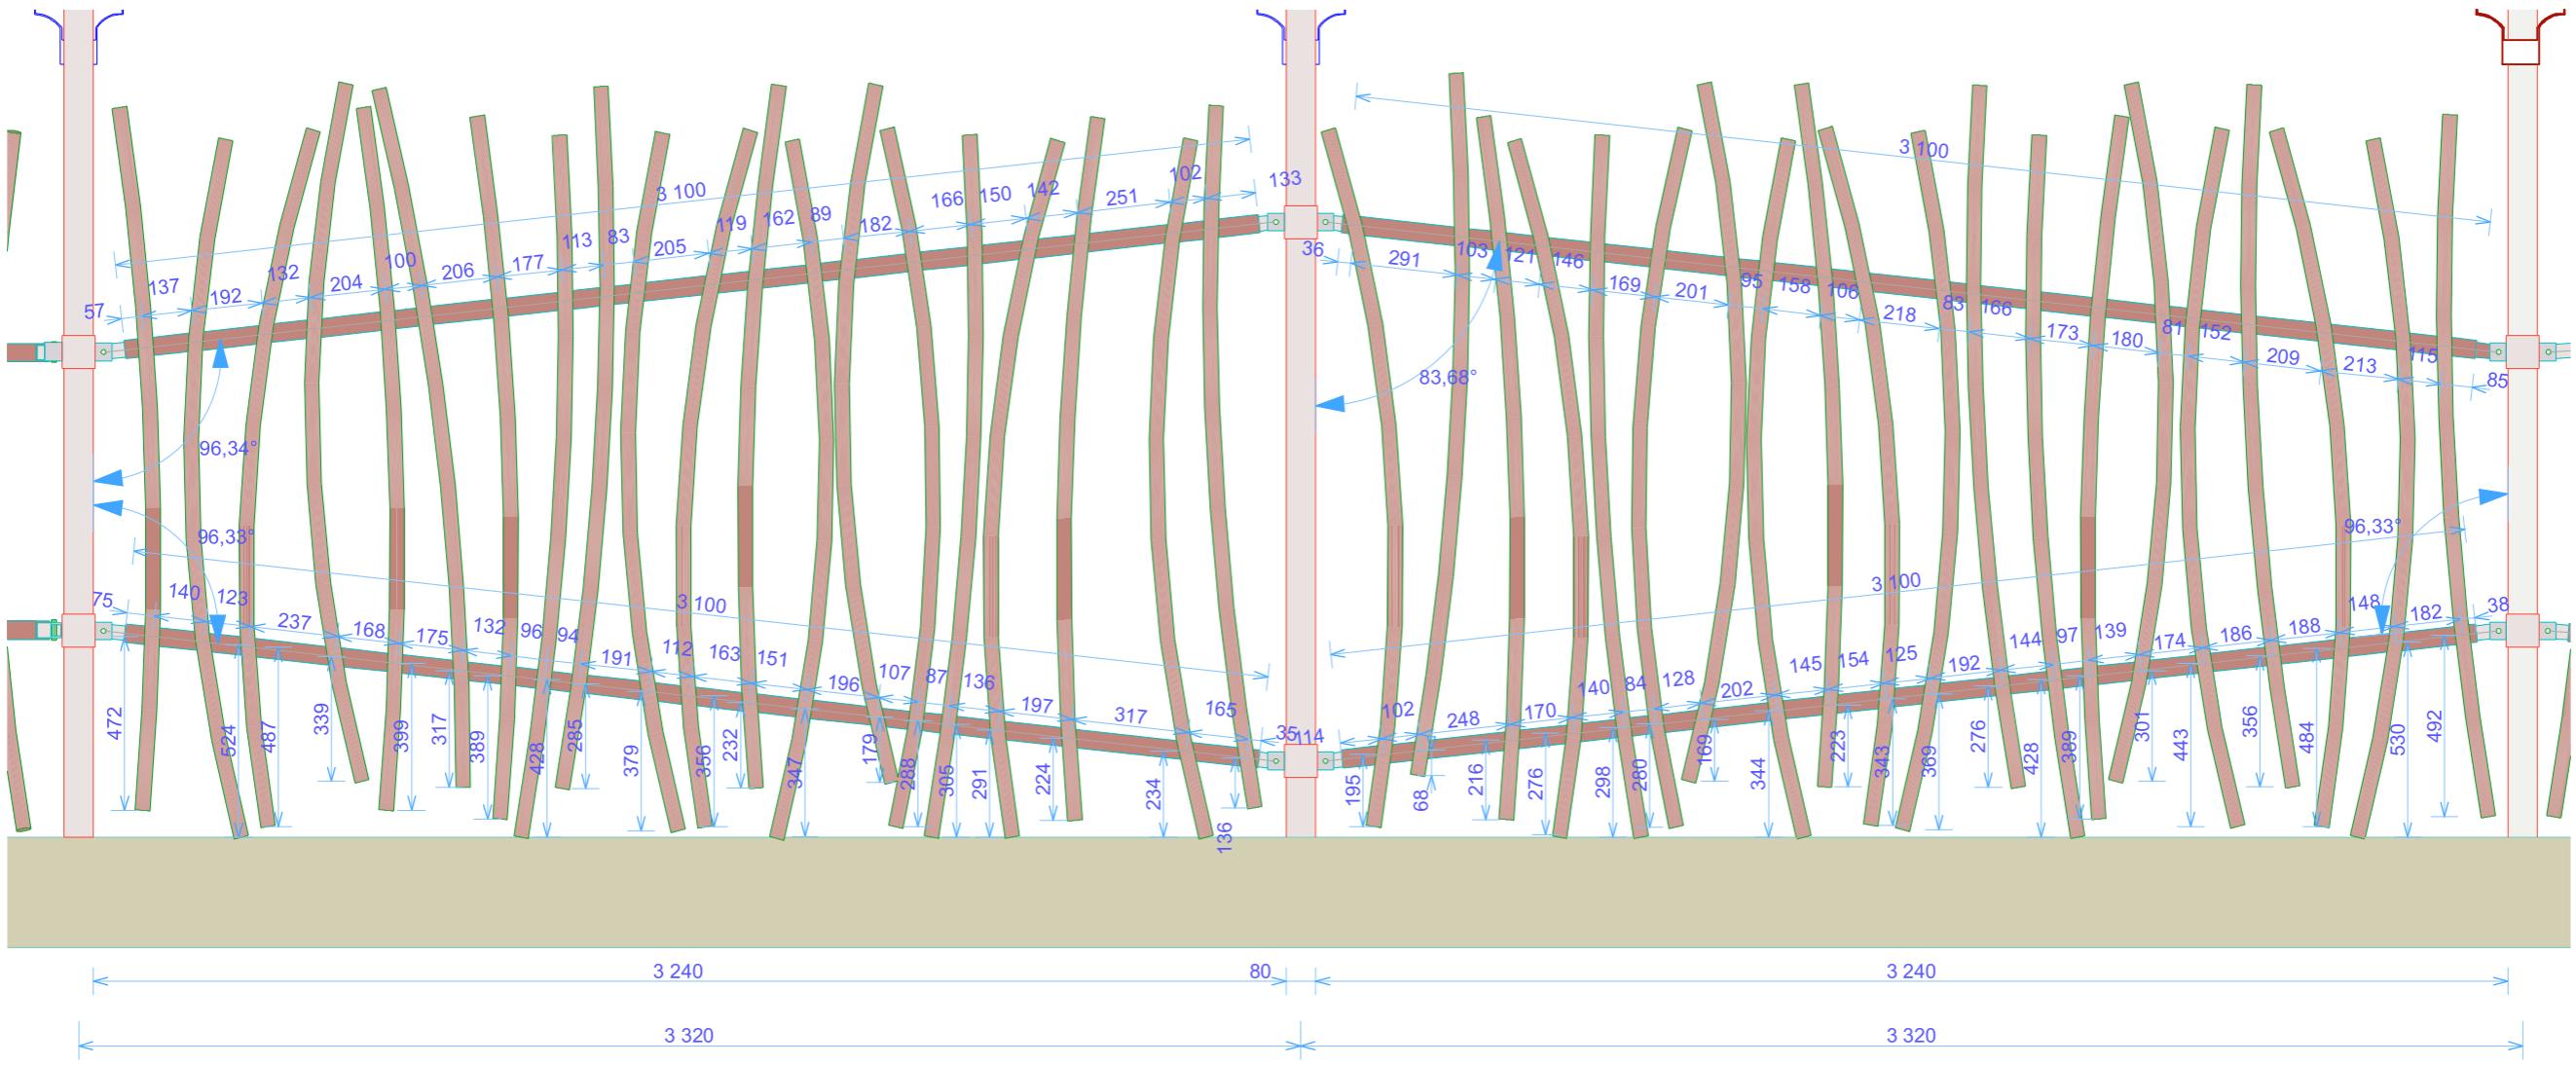

Cloture 4




Cloture 5

4 consoles de liaison
2 consoles d'angle 45° prévues dans détail clôture 3
Poteau et fixation prévu par le storiste

Echelle 1/20




Détails clotures 4 et 5

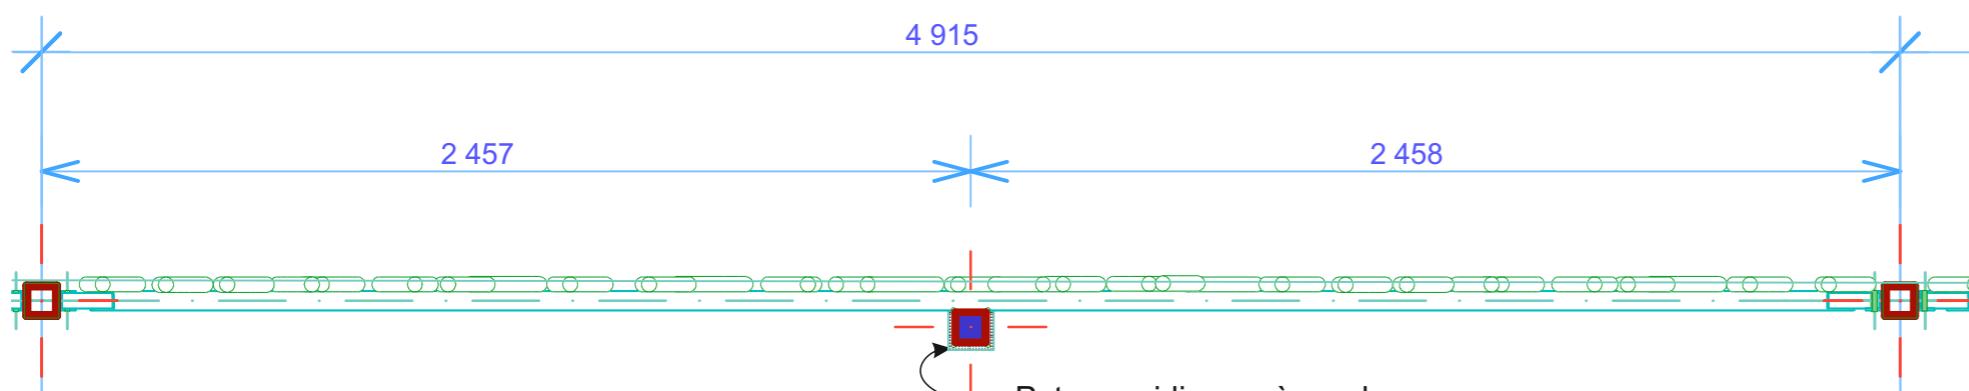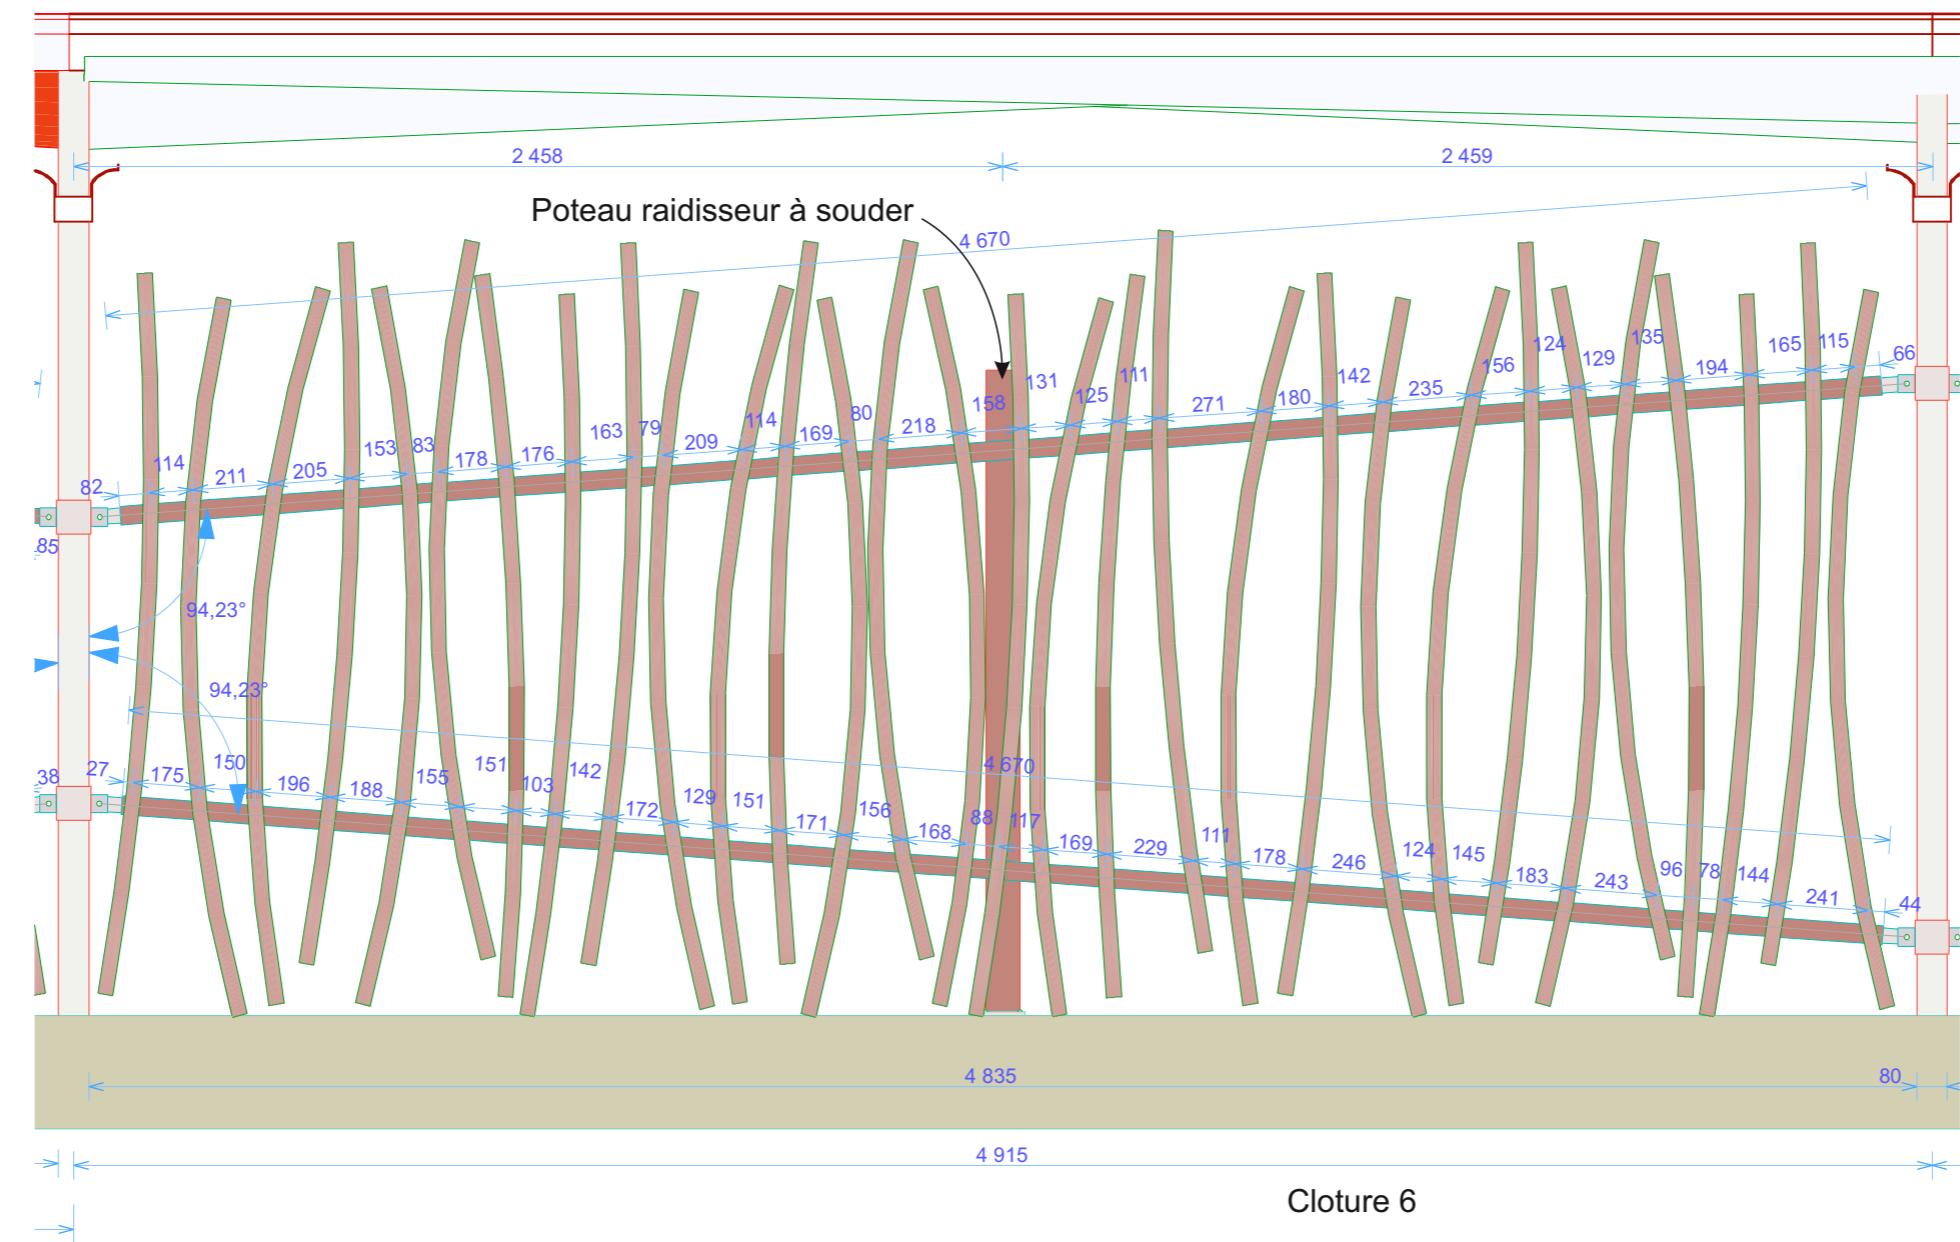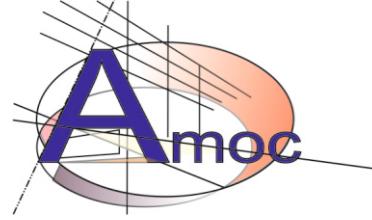


Vue en plan

Détails clôtures 6

Echelle 1/20



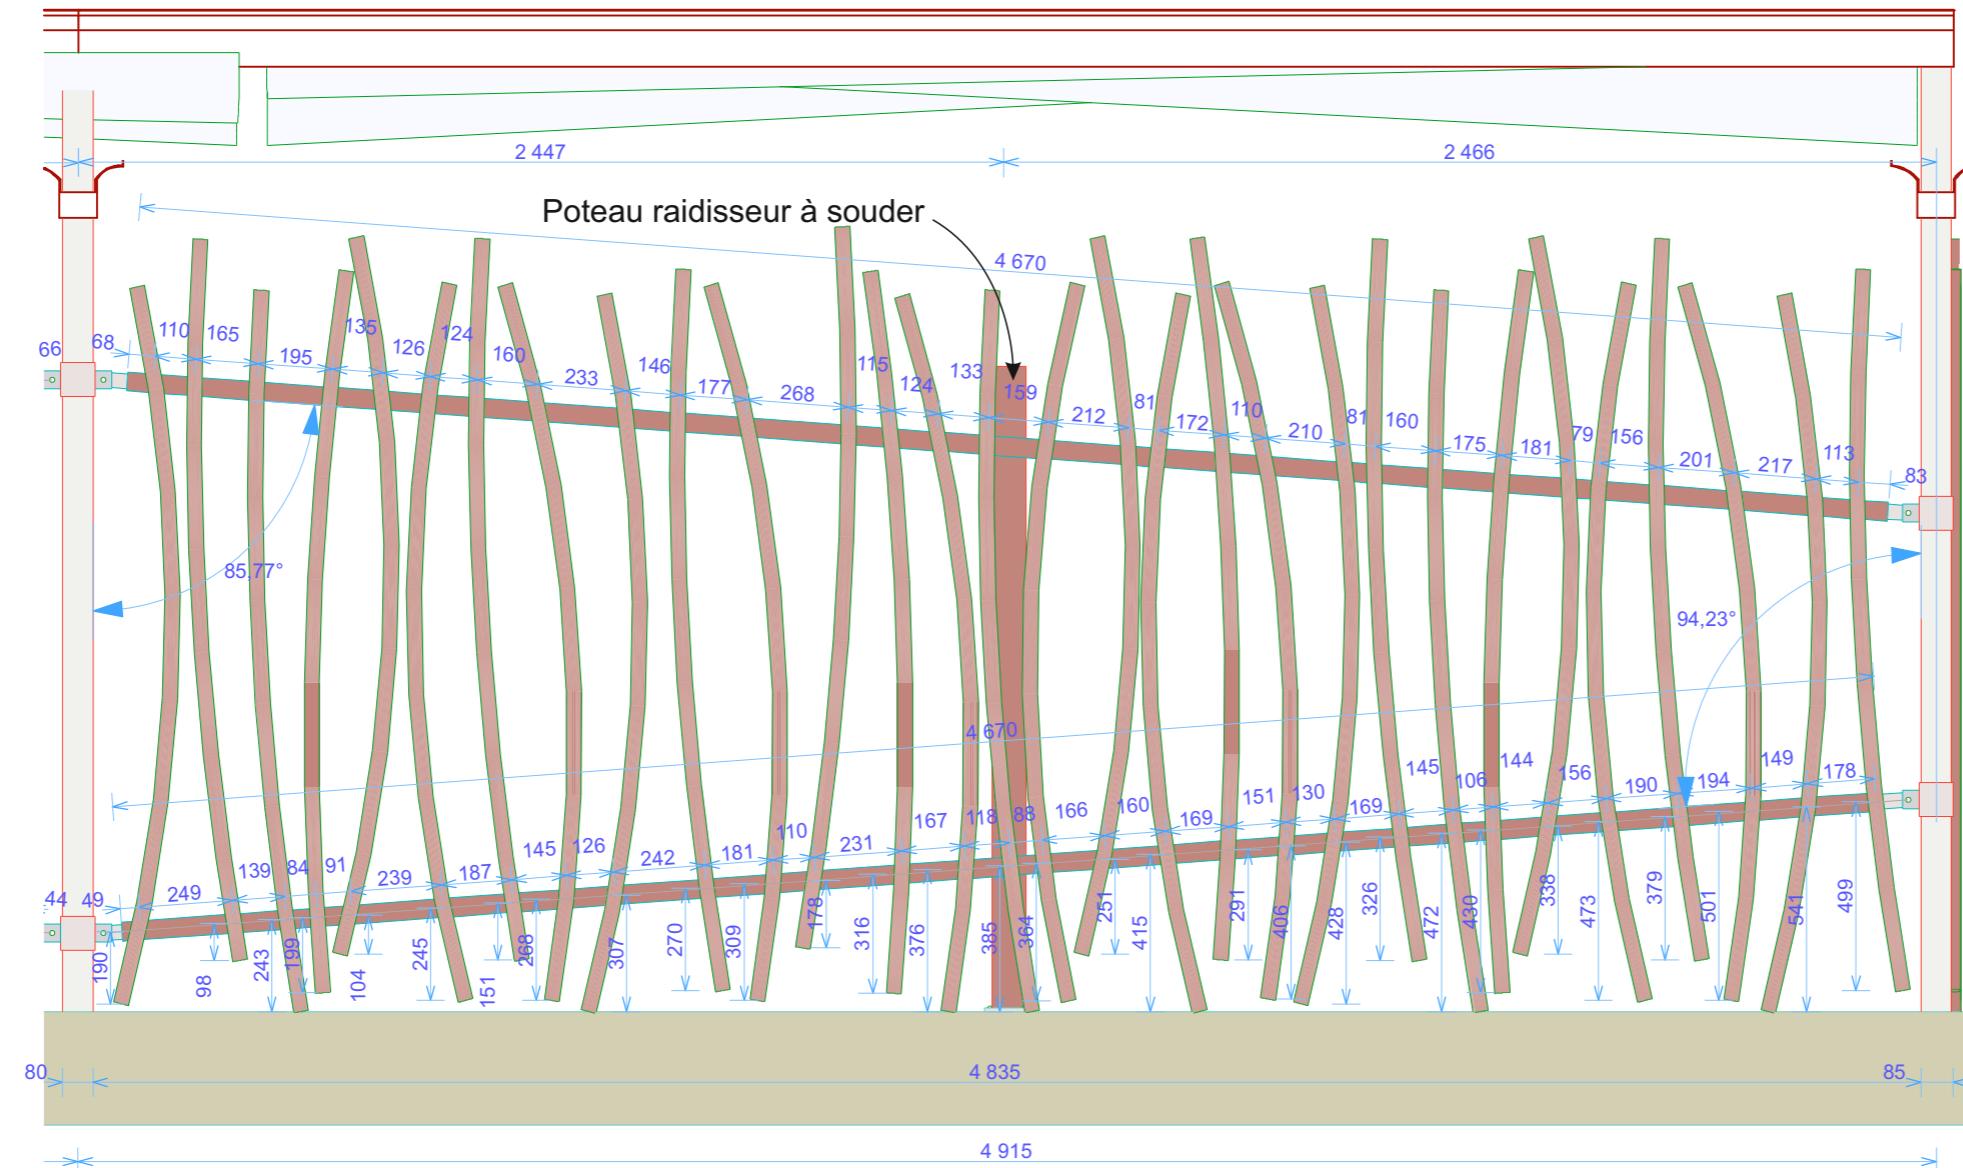


2 consoles d 'angle à 90°
1 Poteau raidisseur 80x80ht 1.90 avec platine
2 consoles de liaison prévues dans détail clôture 6
2 Poteaux et fixation prévu par le storiste

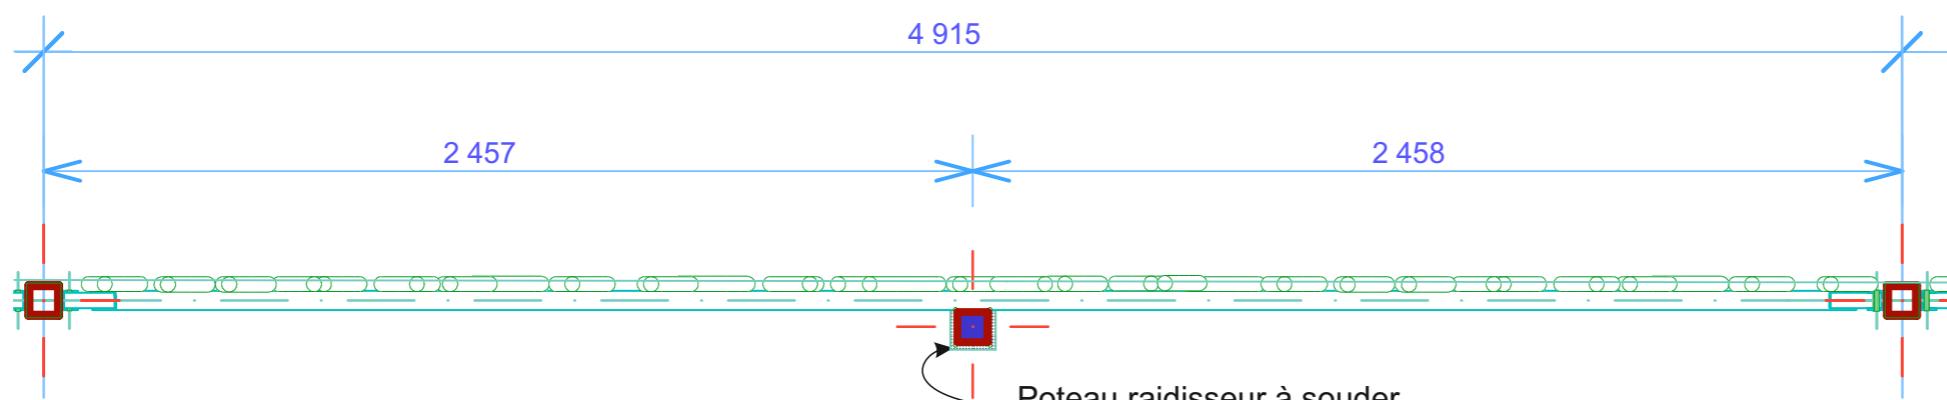

Echelle 1/20


Détails clôtures 7

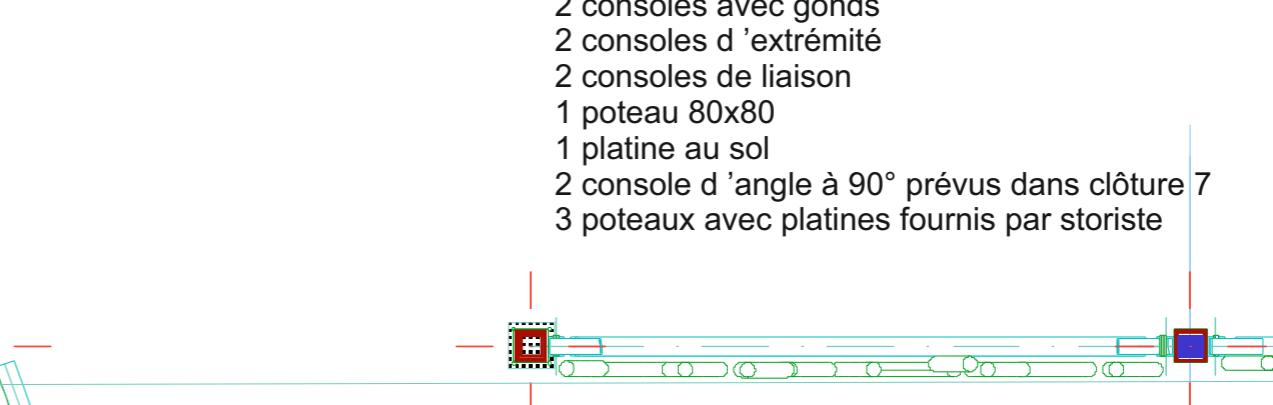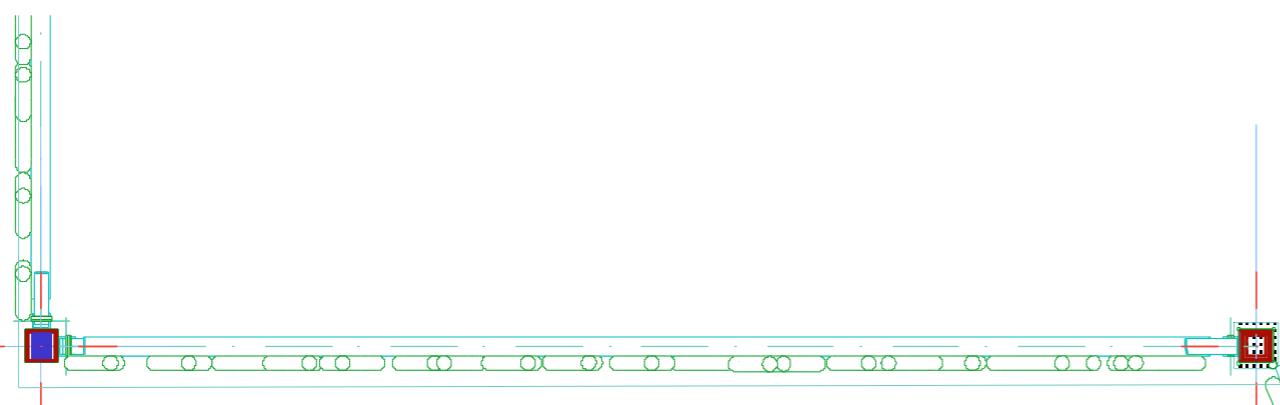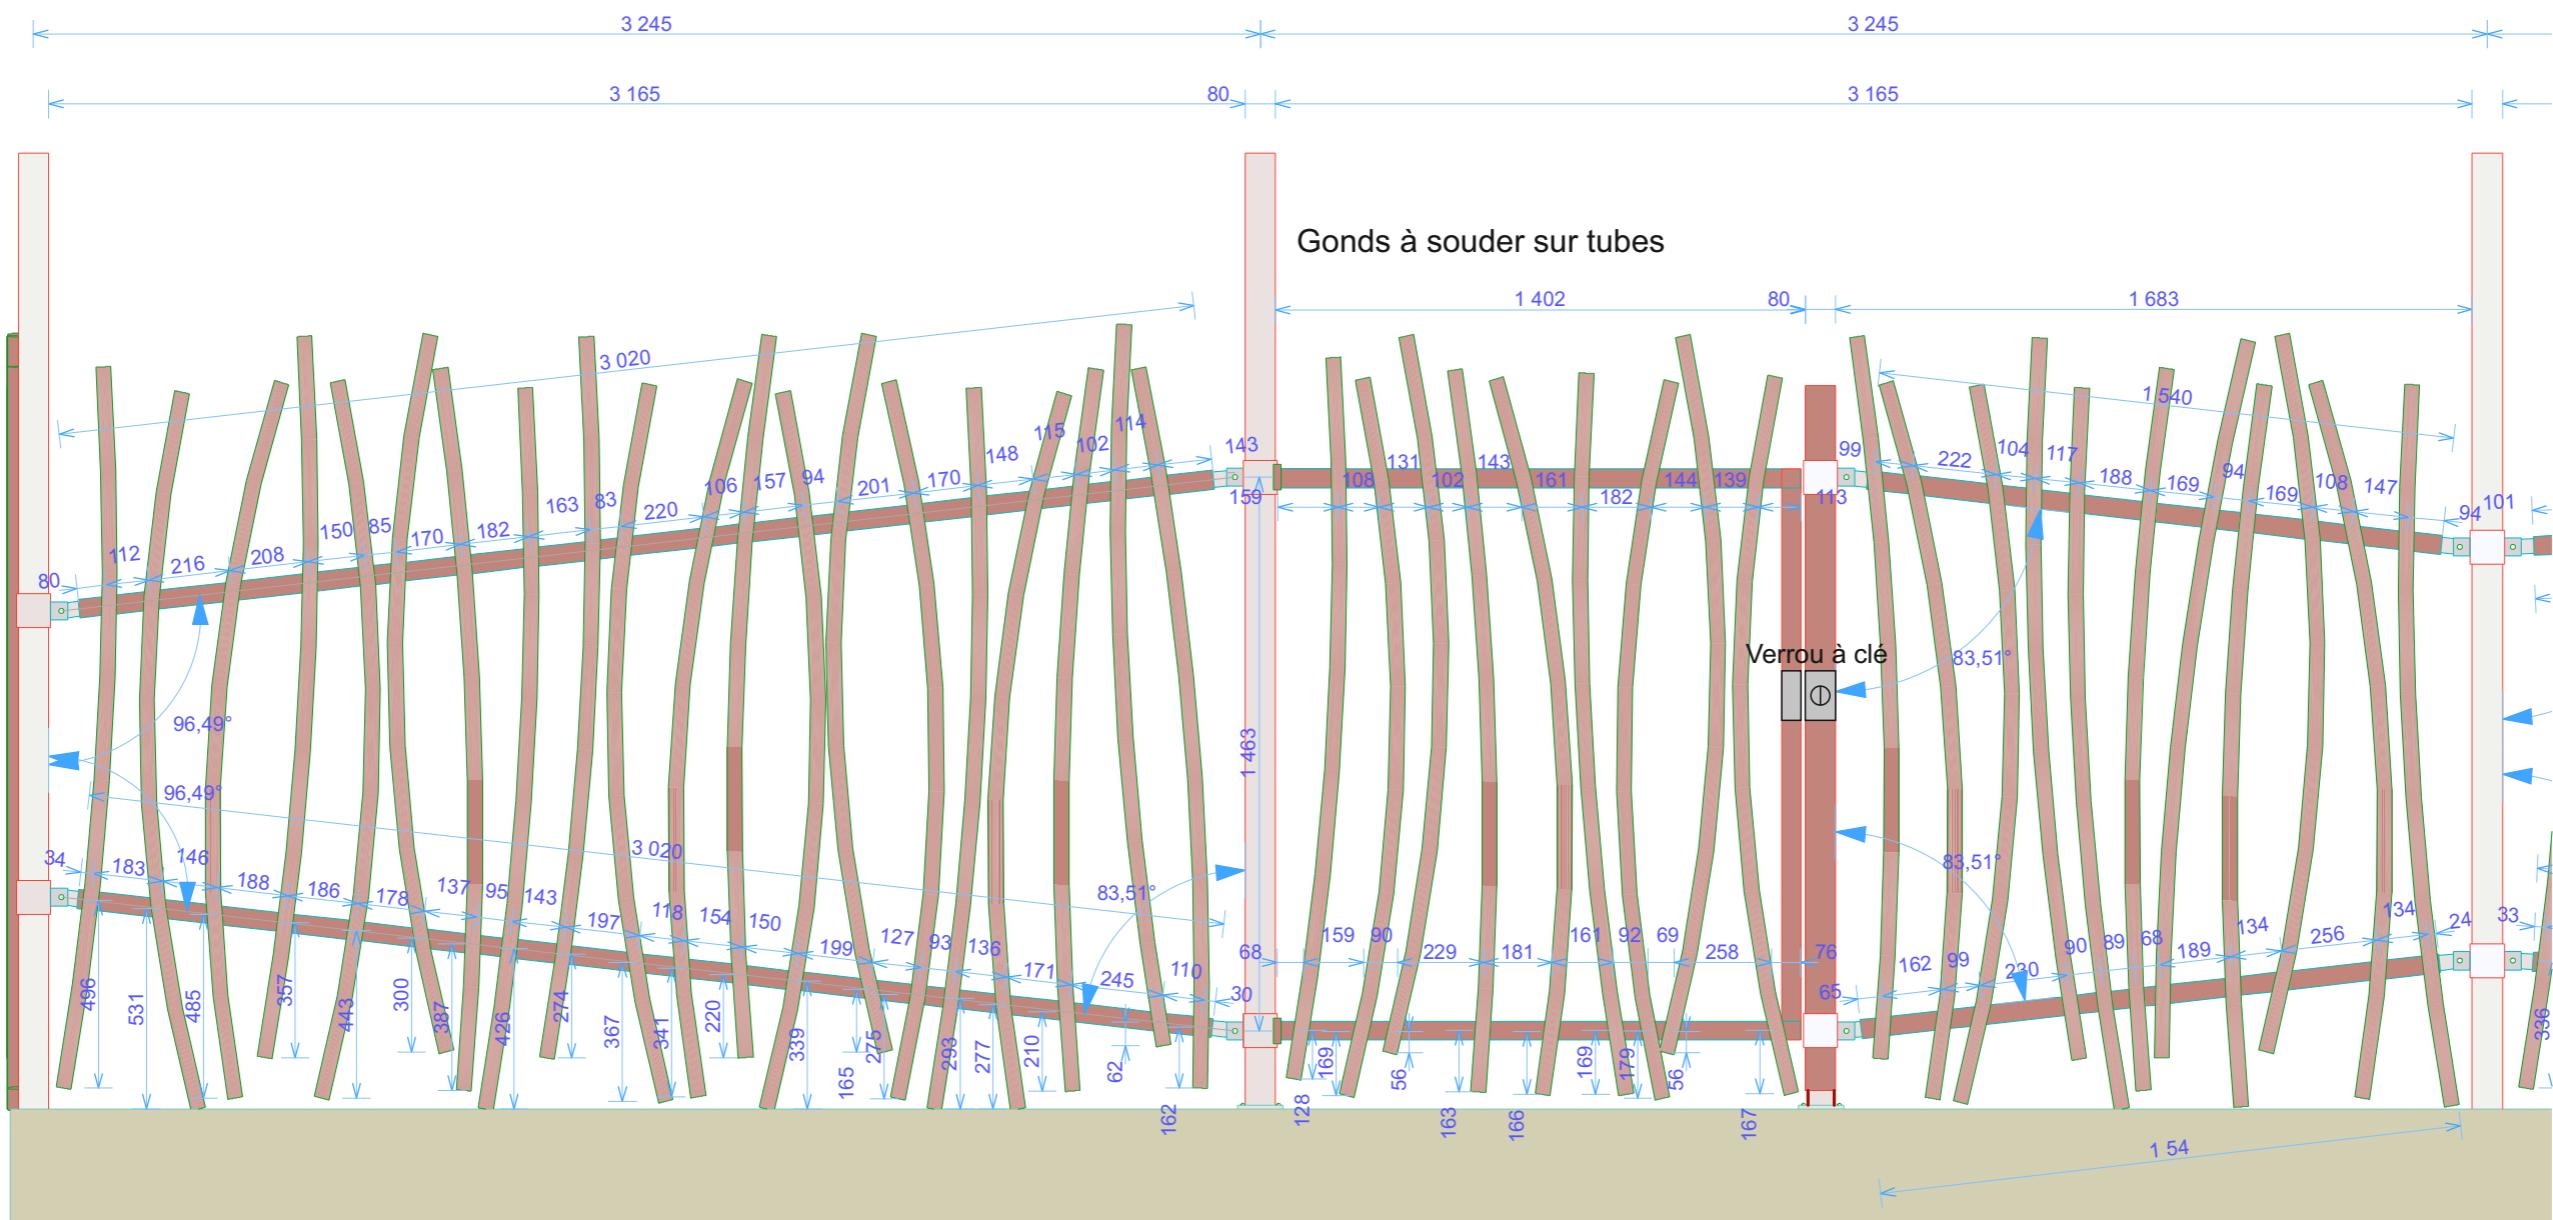

2 consoles avec gonds
2 consoles d 'extrême
2 consoles de liaison
1 poteau 80x80
1 platine au sol
2 console d 'angle à 90° prévus dans clôture 7
3 poteaux avec platines fournis par storiste

Echelle 1/20


Détails clôtures 8 et 9 avec portillon 1

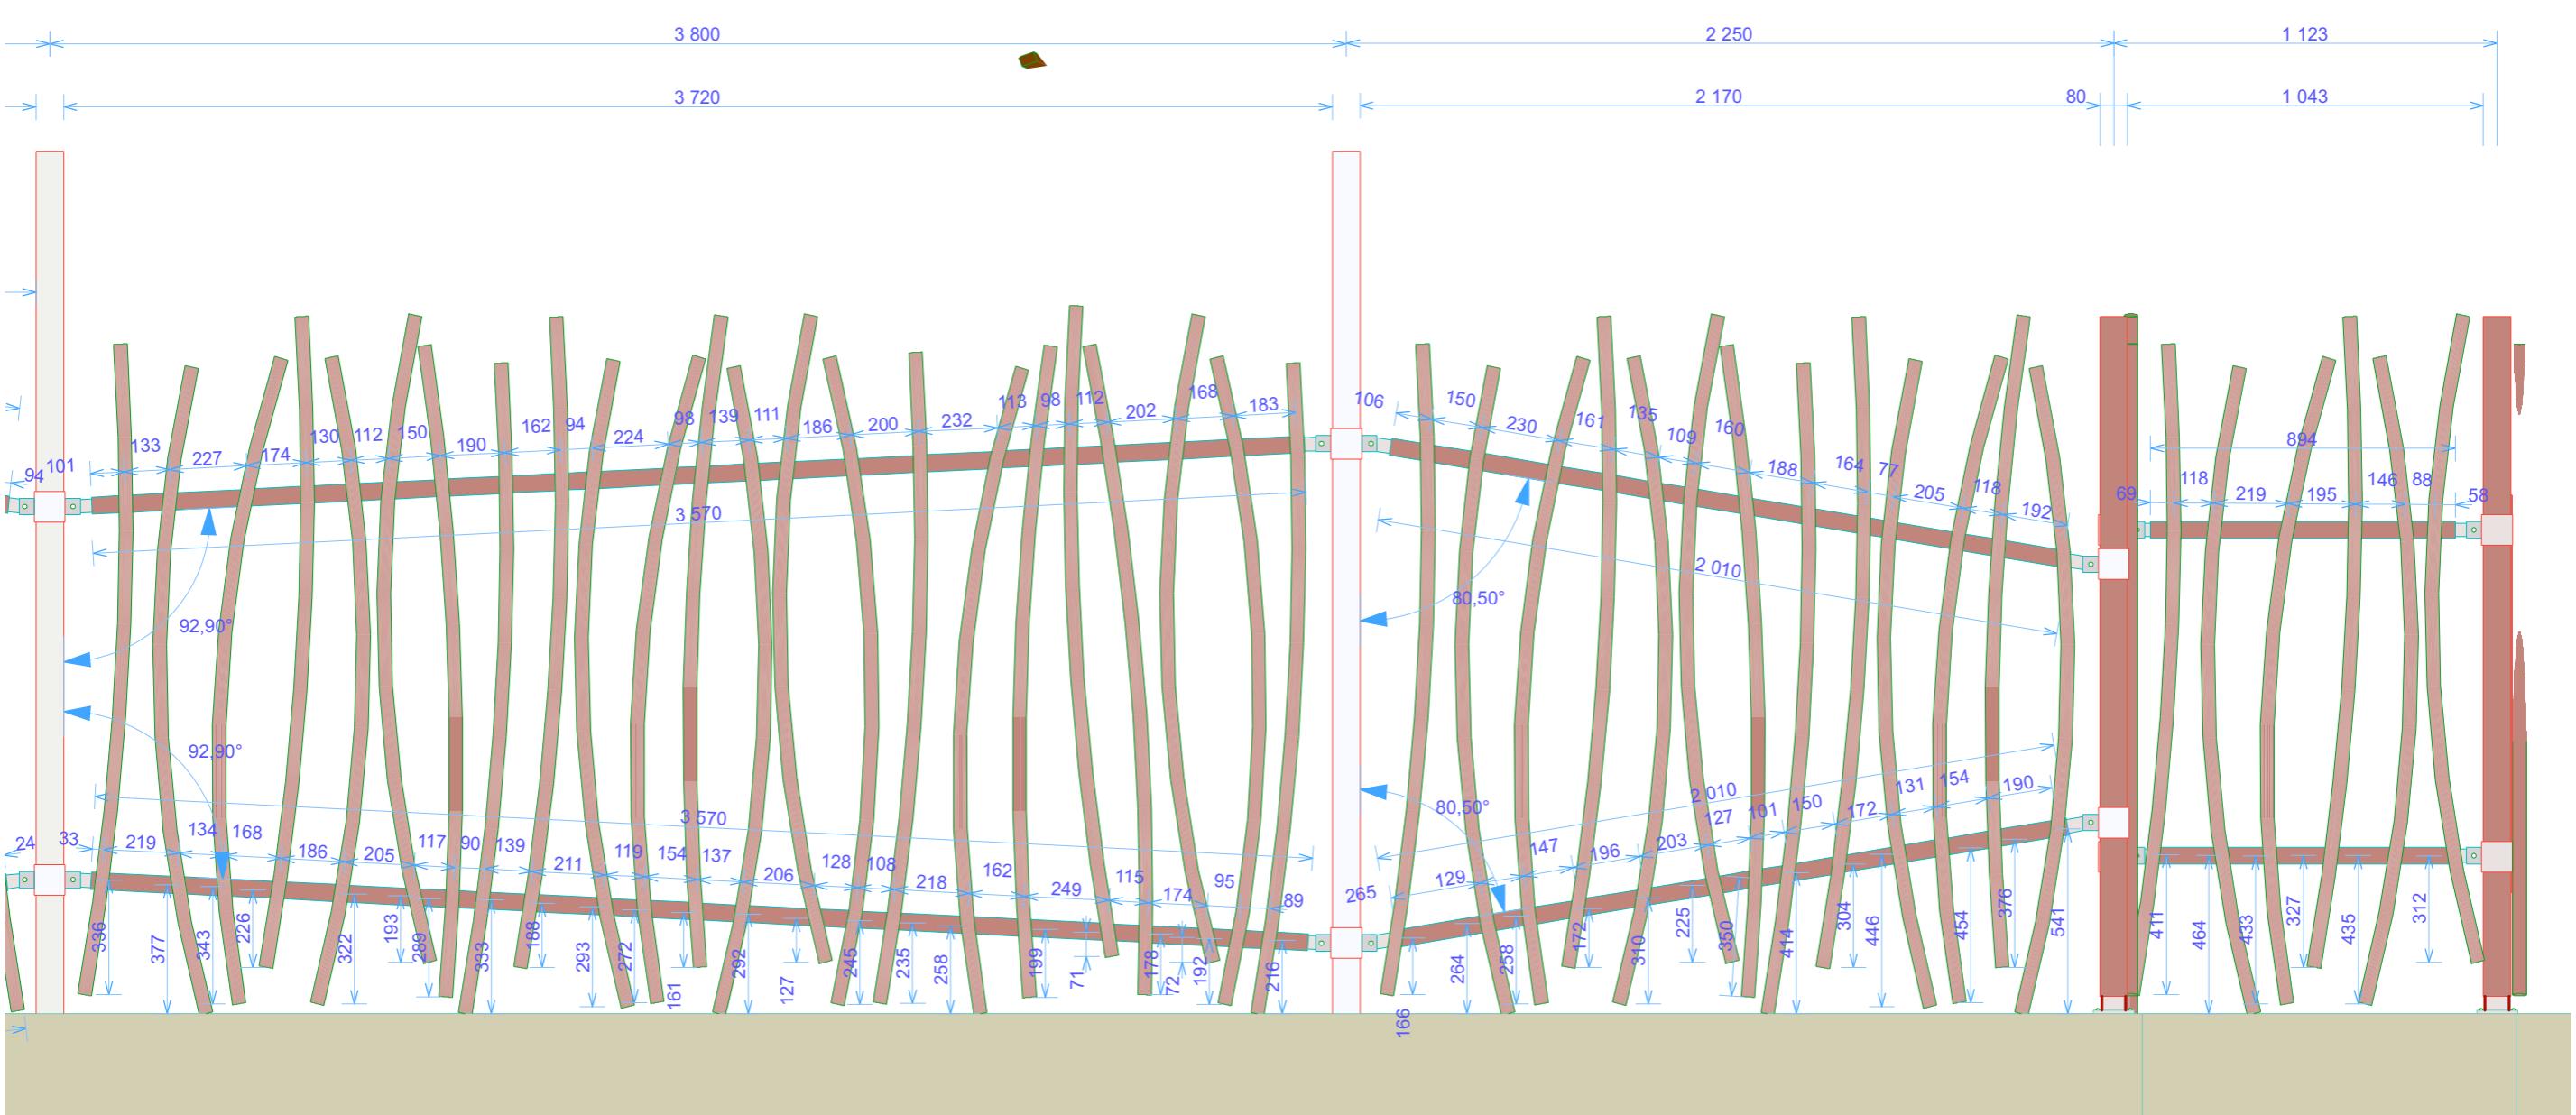

Clôture 10

Clôture 11


Clôture 13

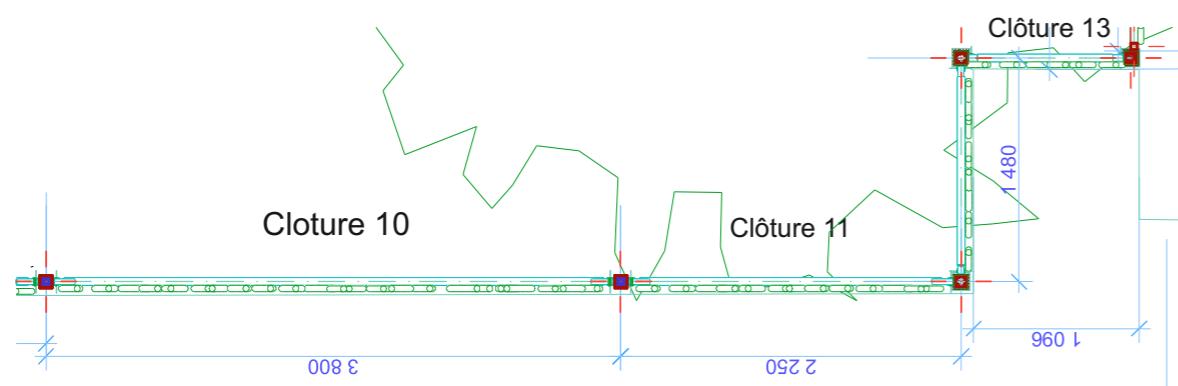

Echelle 1/50

Echelle 1/20


Détails clôtures 8 et 9 avec portillon 1

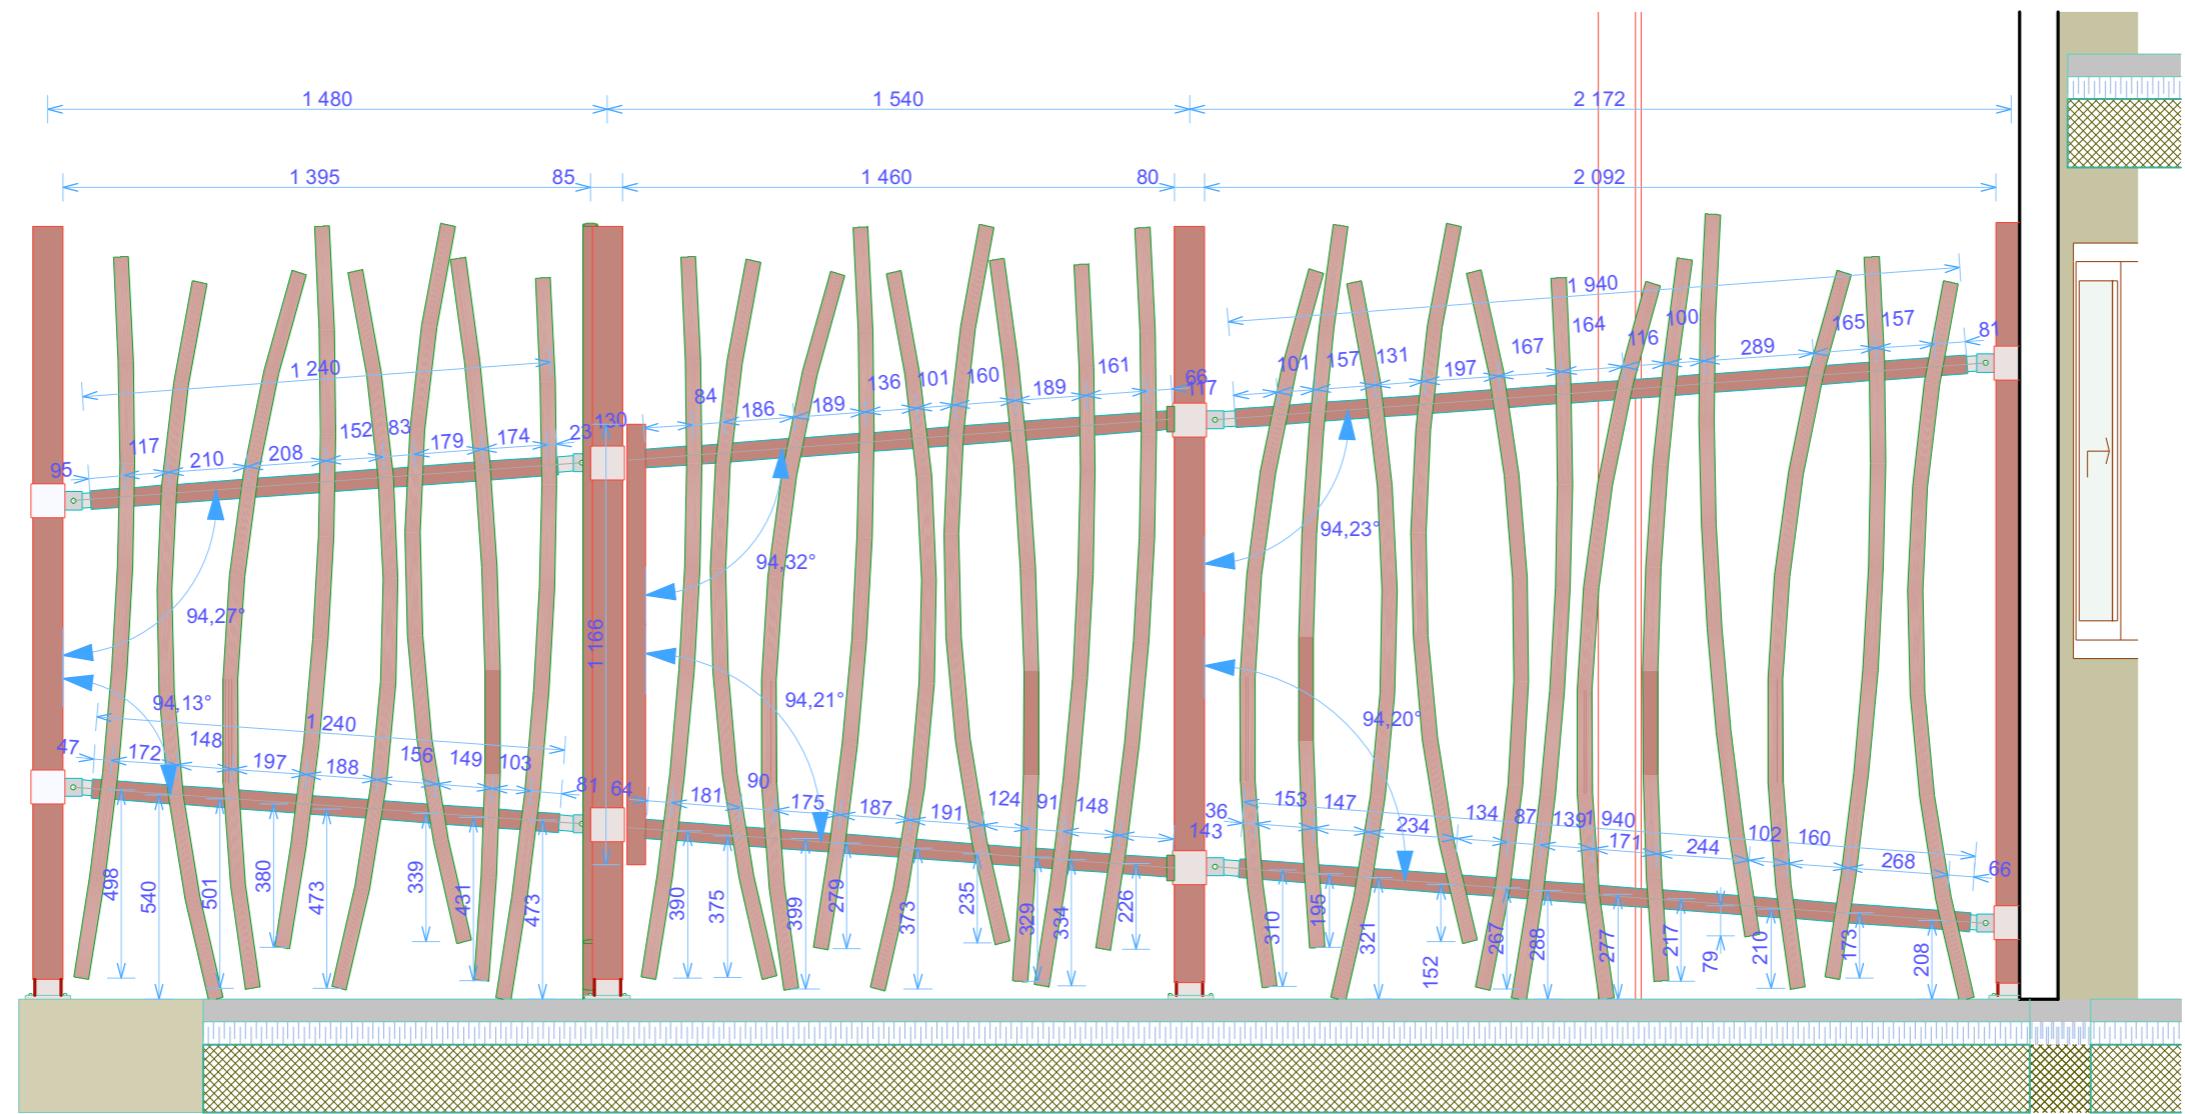

Cloture 12

Portillon

Clôture 14

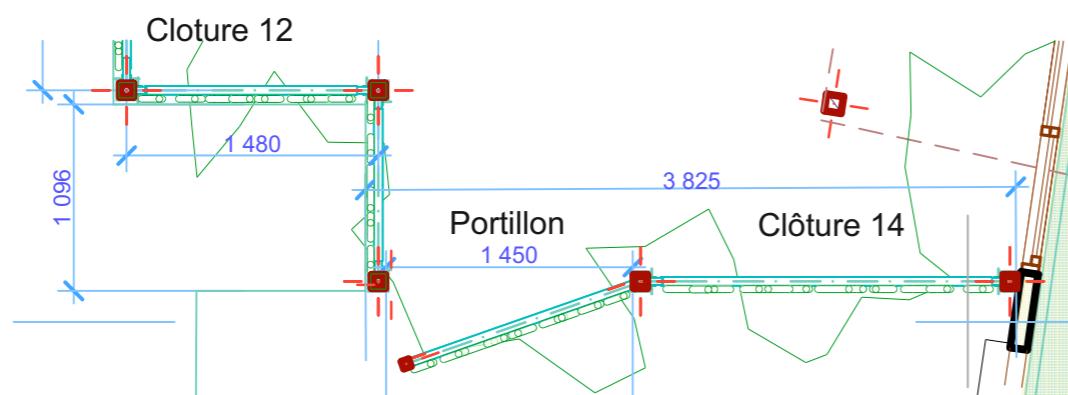

Echelle 1/50

2 consoles d 'angle à 90°
2 consoles d 'extrémitées
3 poteaux 80x80
3 platines au sol
2 consoles dd 'angle 90° prévues clôture 9
2 poteaux avec platines fournis par storiste

Echelle 1/20

Détails clôtures 12 et 14 avec portillon 2